




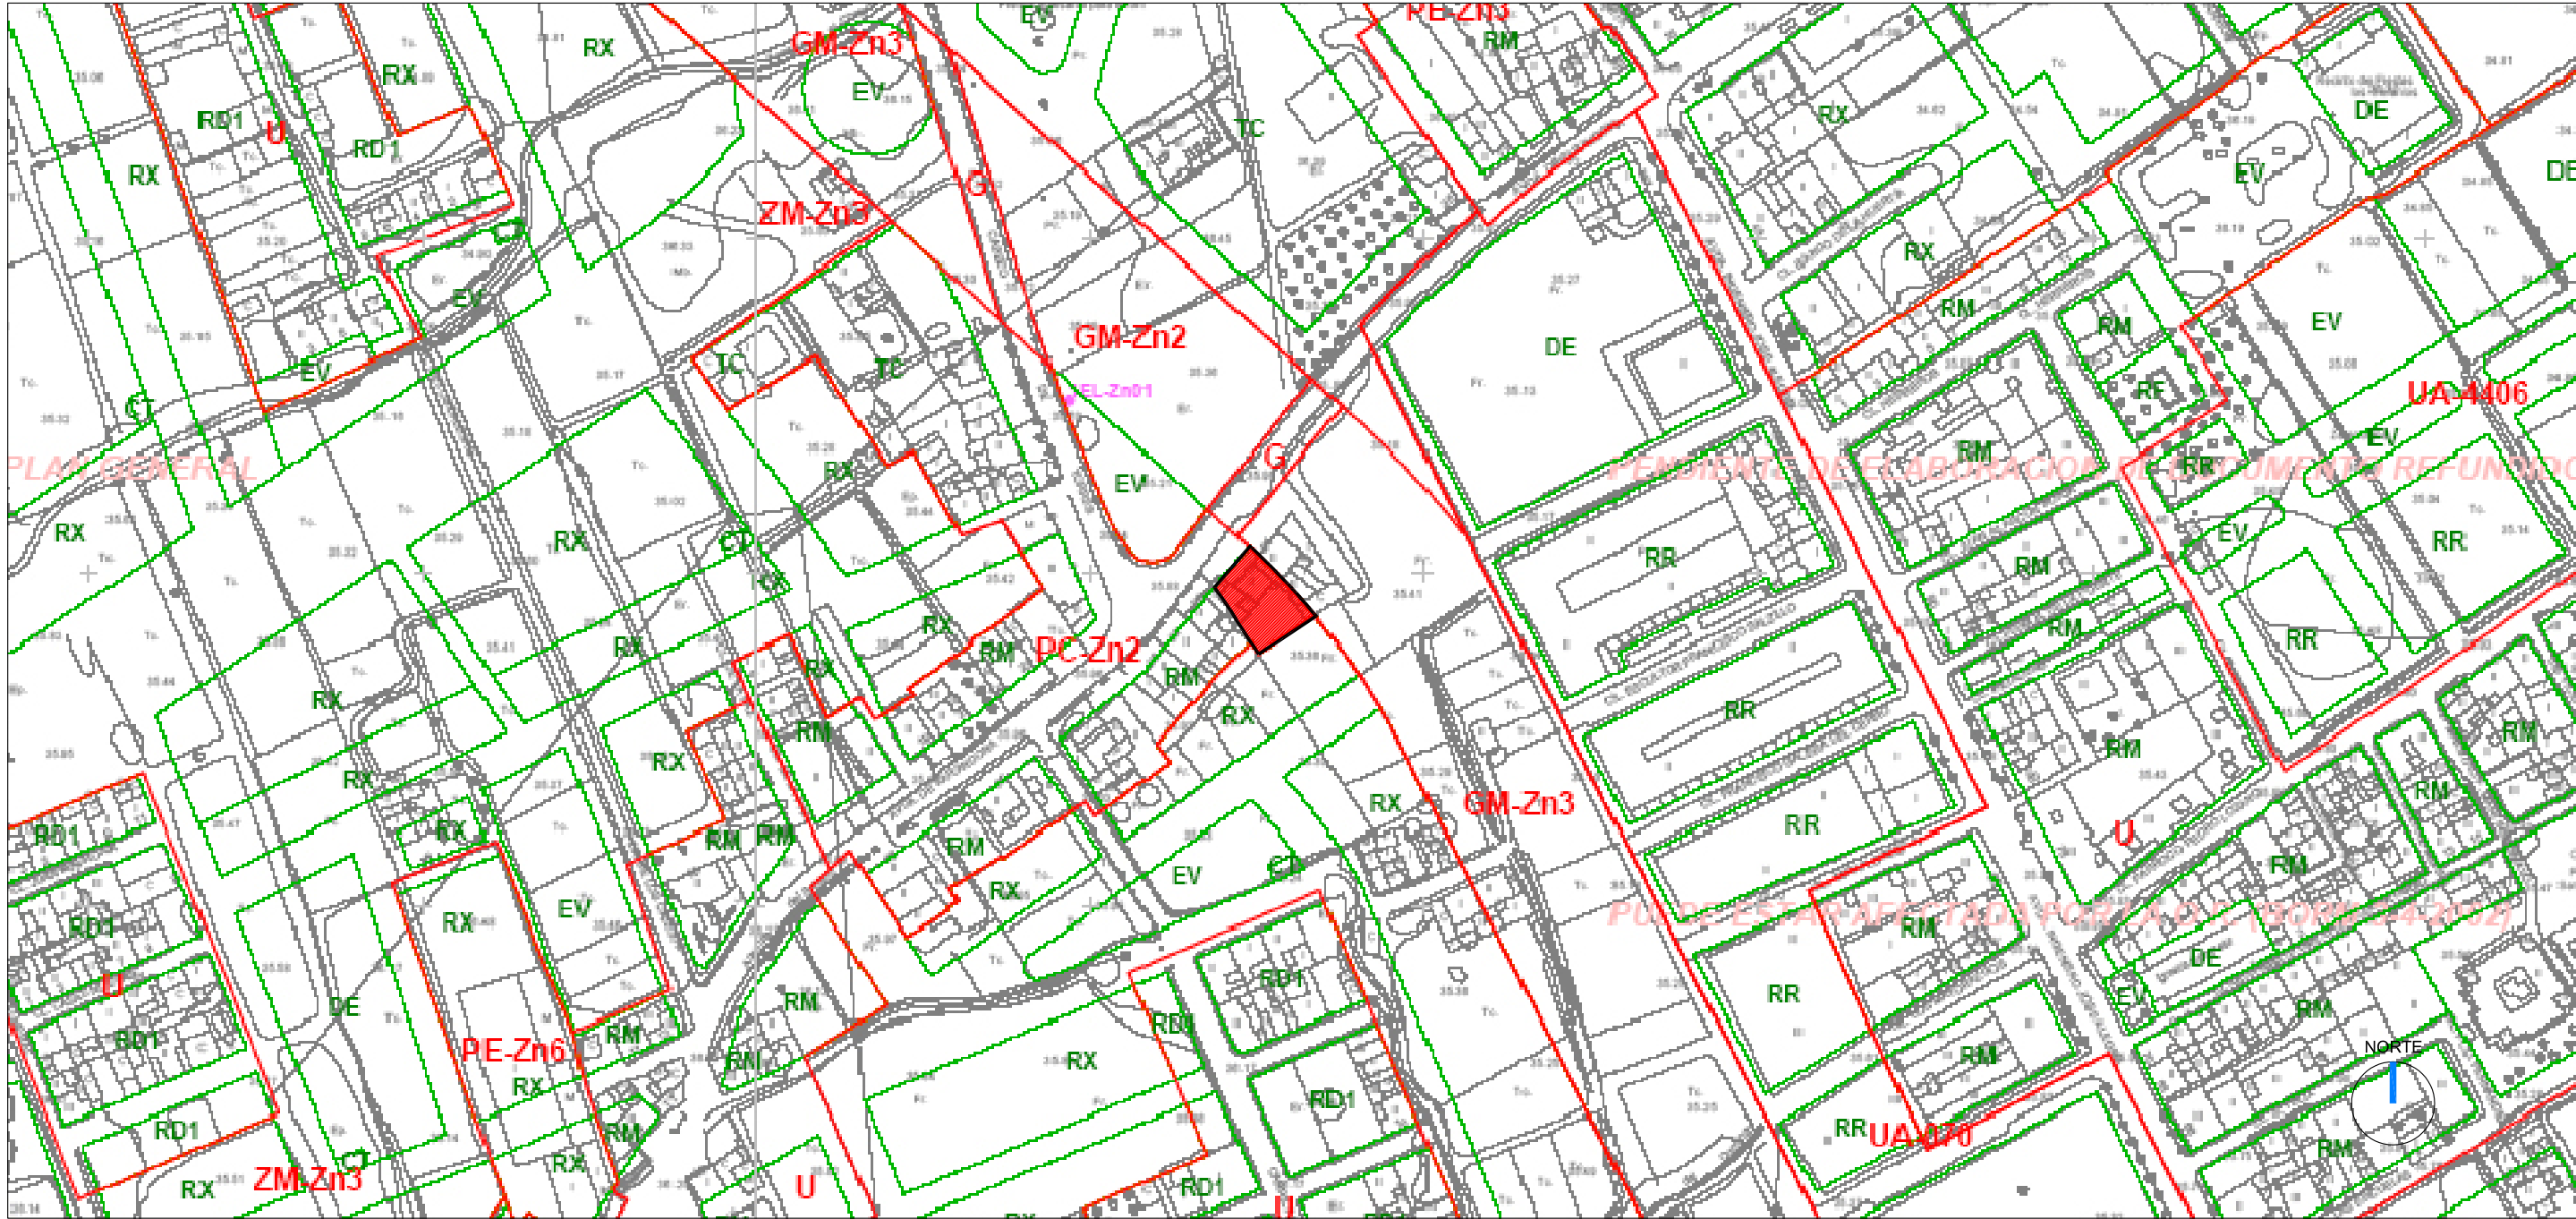

PLANO	PLANO DE ZONIFICACIÓN	EXPTE 598 - 09	ESCALA 1:2000	Nº 01
PROYECTO	B DE 11 VIVIENDAS, LOCALES, GARAJE Y TRASTEROS	FECHA JULIO - 09	SUSTITUYE A	
PROMOTOR	PROMARHOGAR INFANTE S.L.	 VISADO Normal Visado Telemático Colegio Oficial de Arquitectos de Murcia Autores: JUAN SANCHEZ CARRILLO 16/07/2009 155530/40727 MMPG		
SITUACION	AV/ MIGUEL INDURAIN Y OTRA			
JUAN SÁNCHEZ CARRILLO		ARQUITECTO		

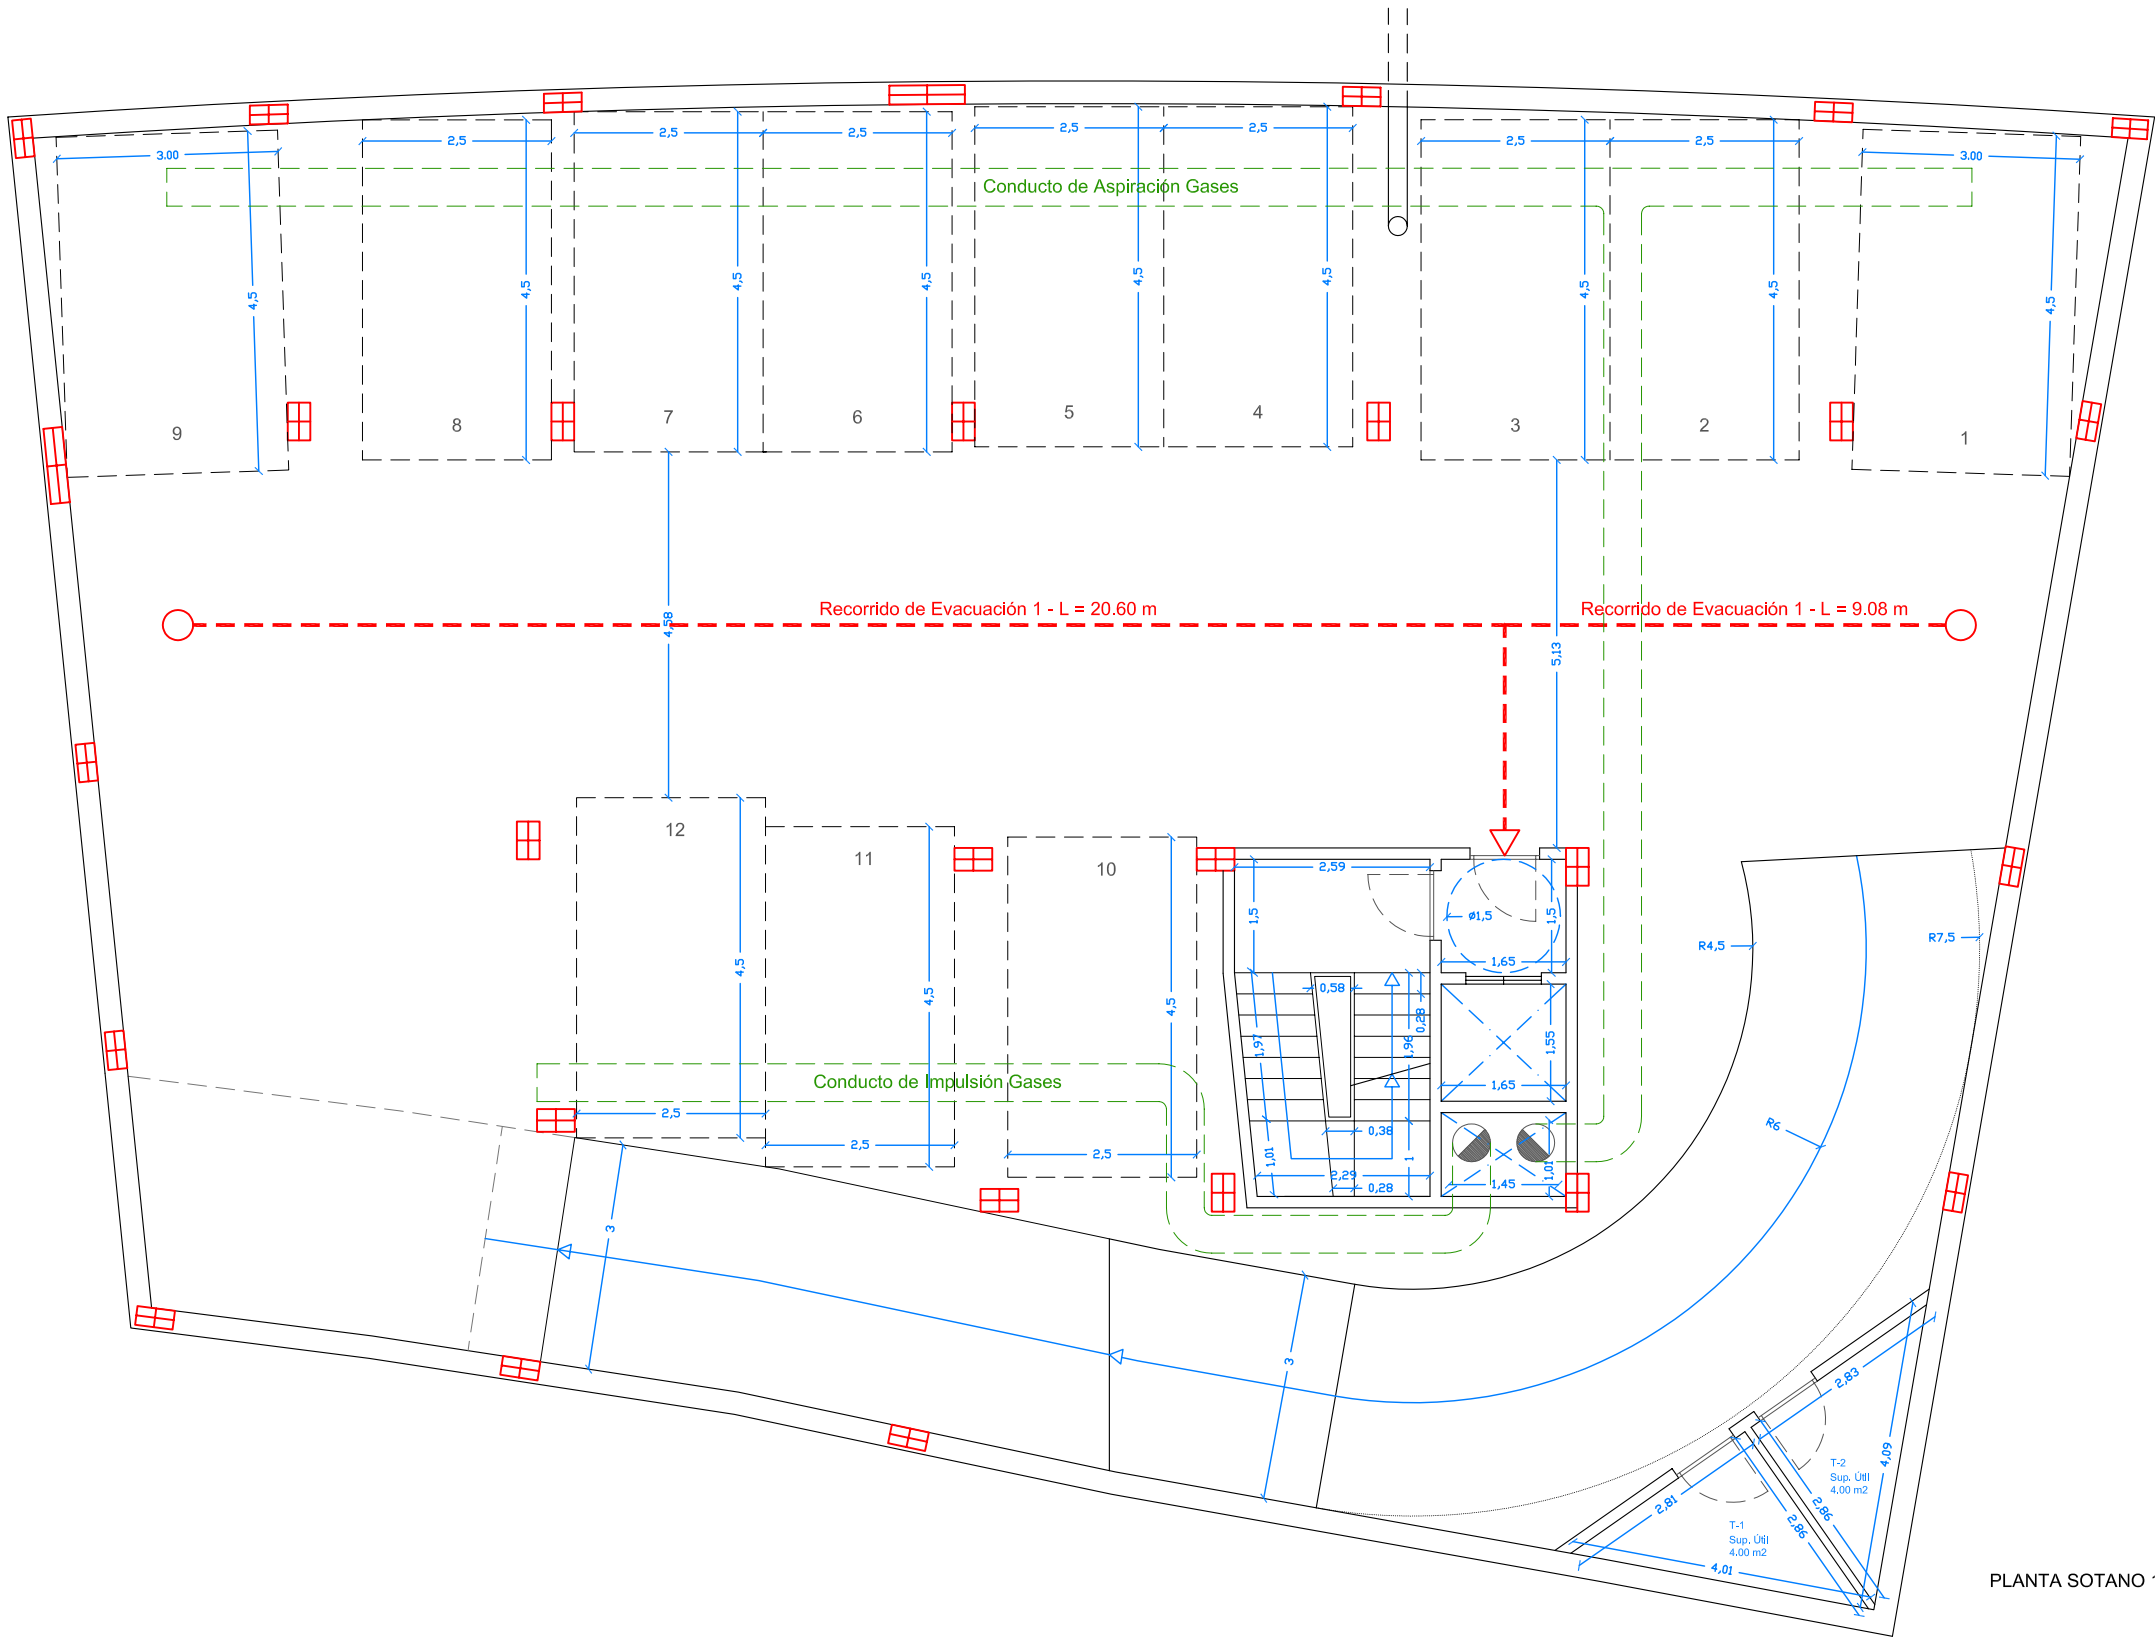


PLANTA SOTANO 1º E/1:100

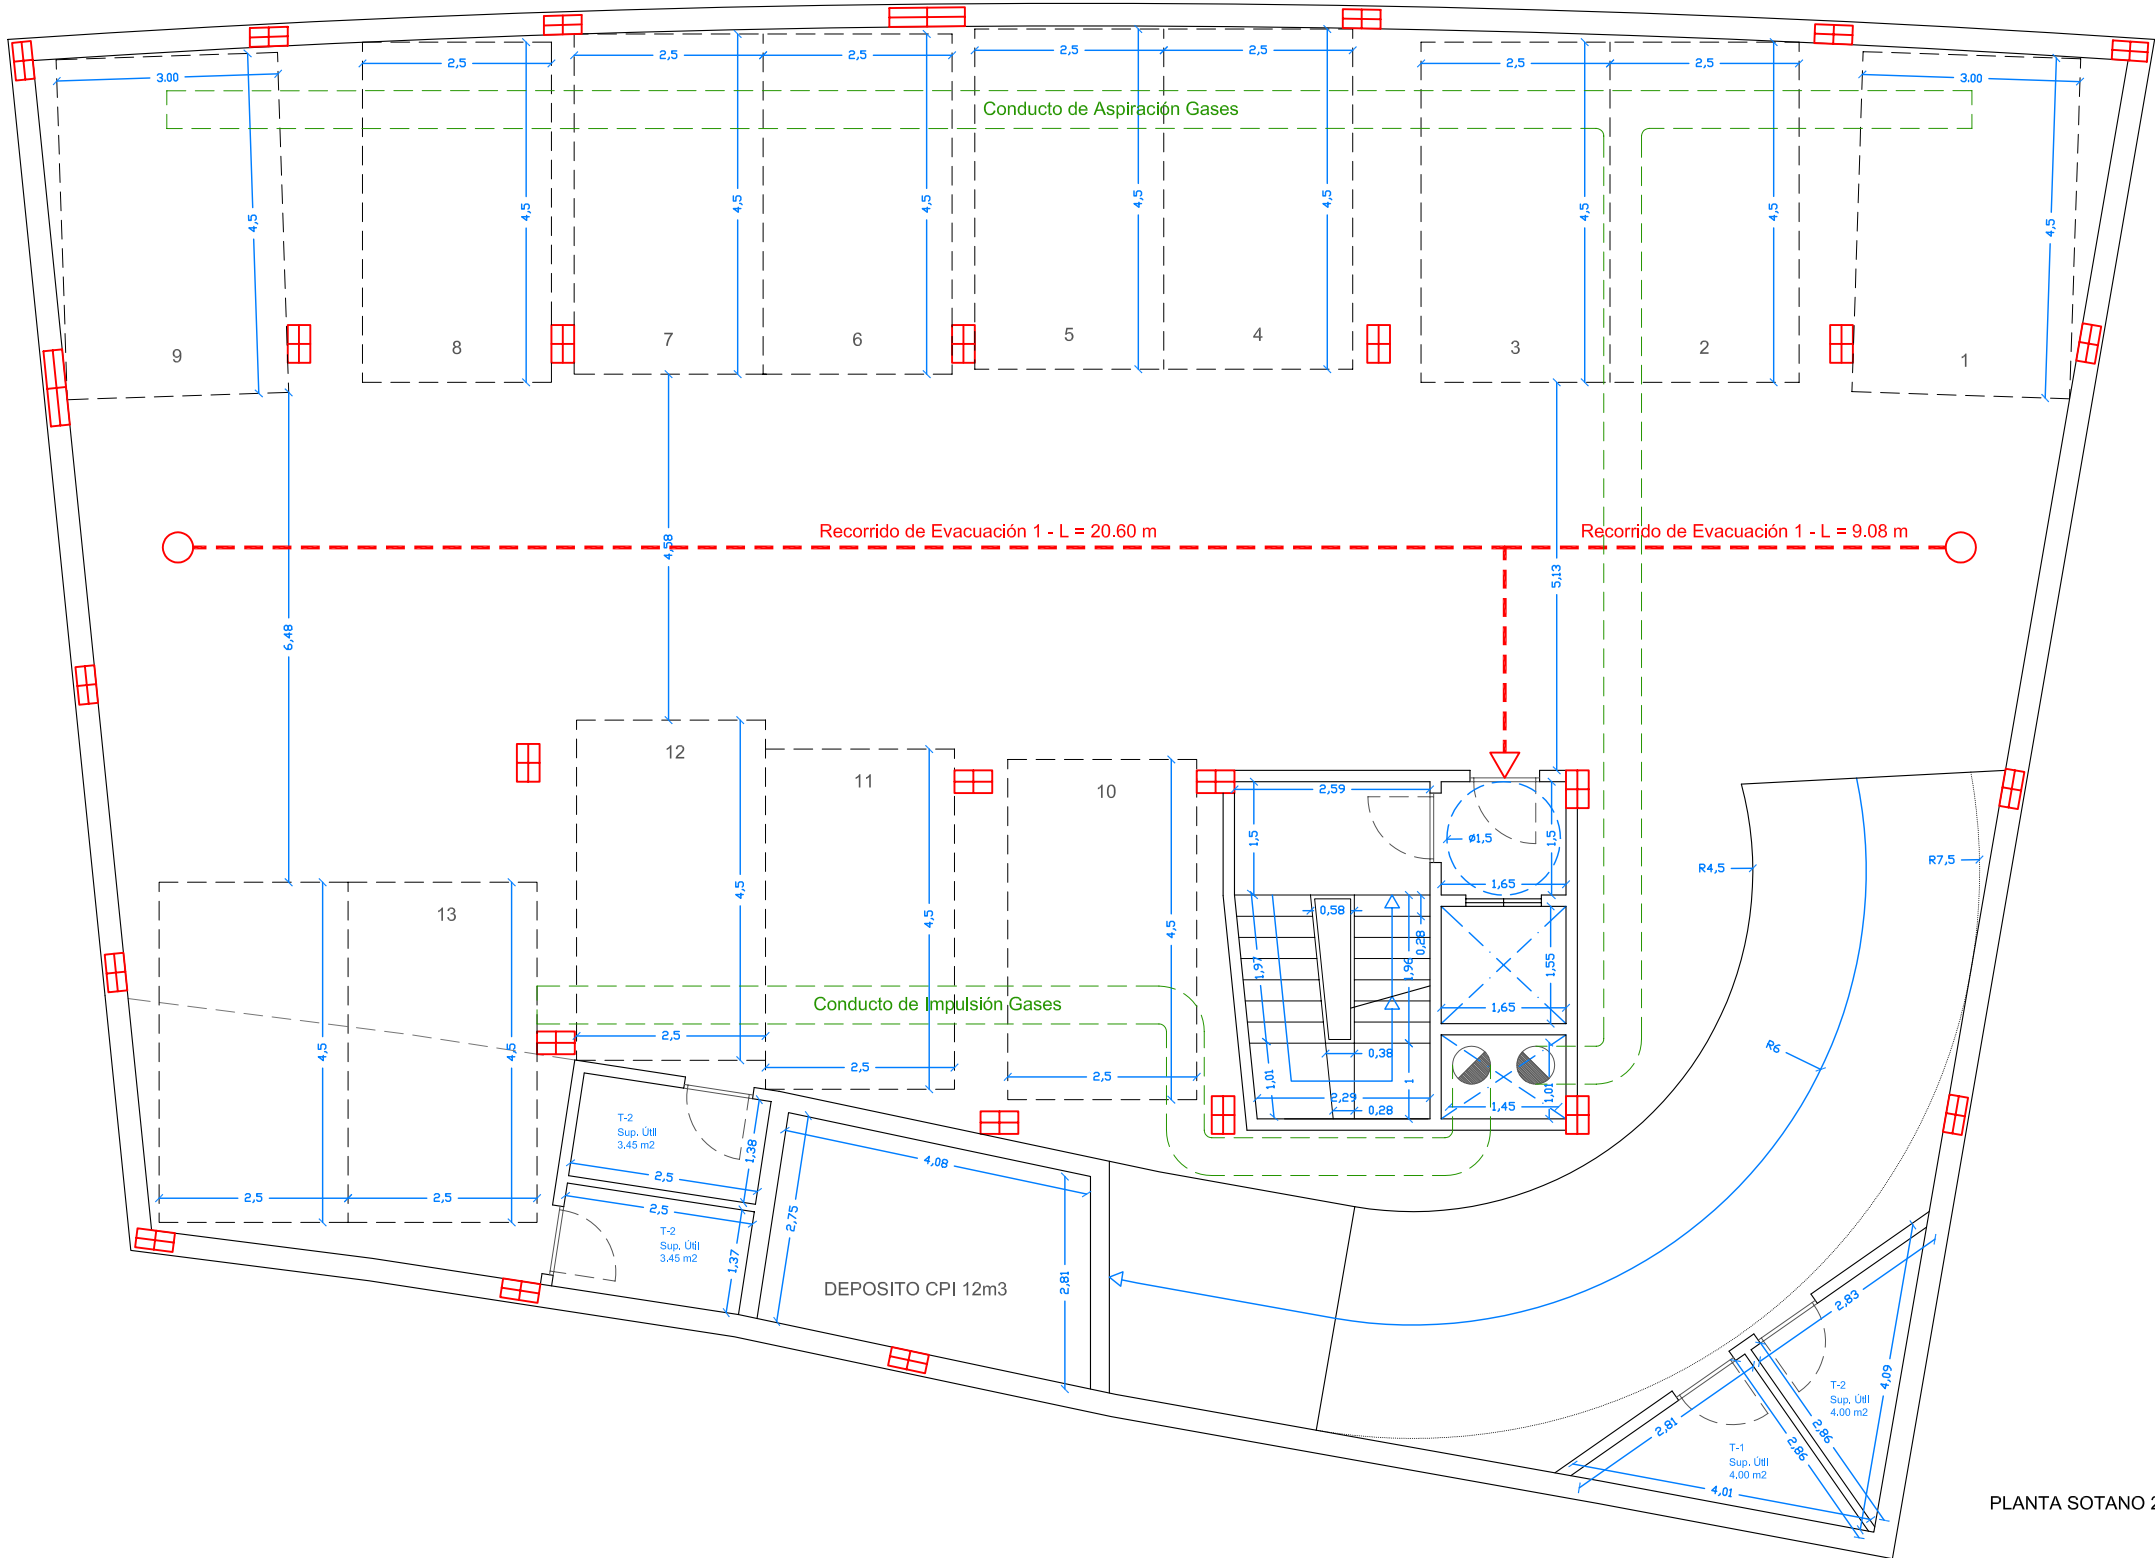

PLANTA SOTANO 2º E/1:100

CUADRO DE SUPERFICIES DE TRASTEROS			
PLANTA	TIPO	SUP. ÚTIL	SUP. CONSTRUIDA
SOTANO 1º	T-1	4.00 m2	5.95 m2
	T-2	4.00 m2	5.95 m2
SOTANO 2º	T-1	4.00 m2	5.95 m2
	T-2	4.00 m2	5.95 m2
	T-3	3.45 m2	4.58 m2
	T-4	3.45 m2	4.58 m2
TOTAL	6 Tras.	22.90 m2	32.96 m2

PLANO	PLANTAS SOTANO 1º Y 2º	EXPRE 598 - 09	ESCALA 1:100	Nº 03
PROYECTO	B DE 11 VIVIENDAS, LOCALES, GARAJE Y TRASTEROS	FECHA JULIO - 09	SUSTITUYE A	
PROMOTOR	PROMARHOGAR INFANTE S.L.	 VISADO Normal Colegio Oficial de Arquitectos de Murcia Visado Telemático Autores: JUAN SANCHEZ CARRILLO		
SITUACION	AV/ MIGUEL INDURAIN Y OTRA			
JUAN SÁNCHEZ CARRILLO		ARQUITECTO		

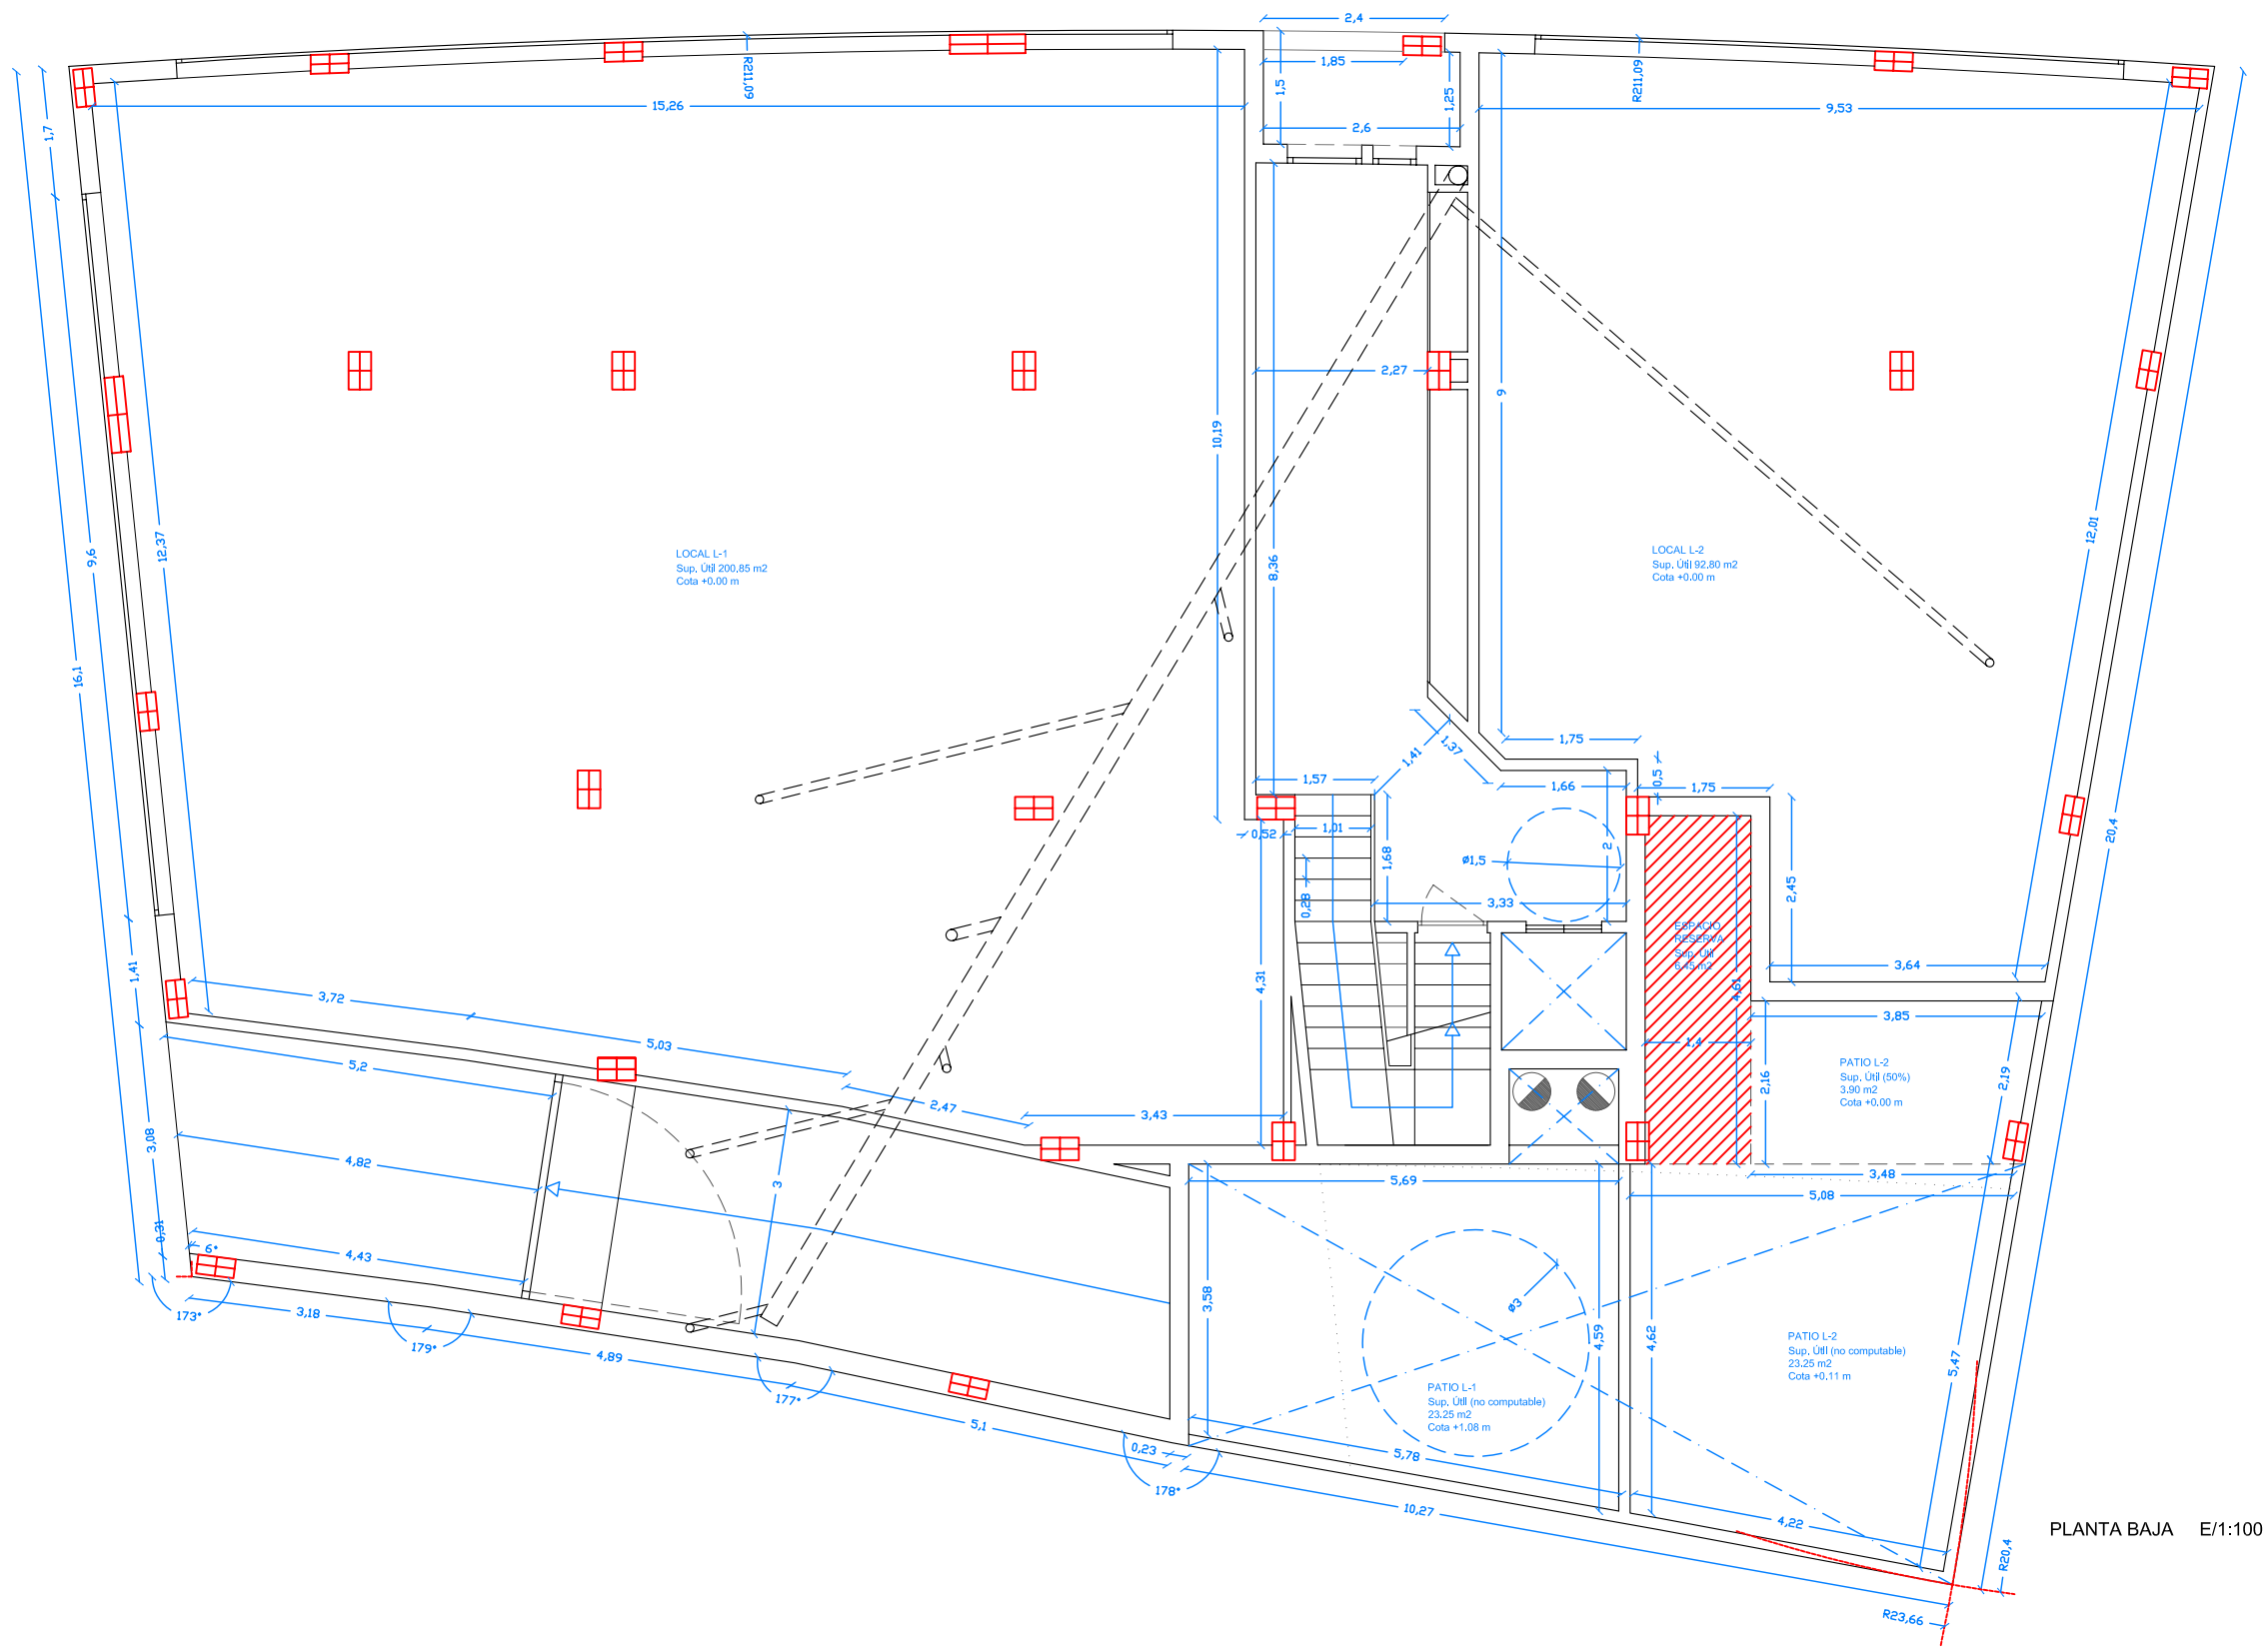


CUADRO DE SUPERFICIES DE LOCALES				
PLANTA	TIPO	SUP. ÚTIL	SUP. CONSTRUIDA	SUP. PATIOS (No computable)
BAJA	L-1	200.85 m2	210.82 m2	23.25 m2
	L-2	96.70 m2	103.47 m2	23.25 m2
TOTAL	2 Loc.	297.55 m2	314.29 m2	46.50 m2

PLANO	PLANTA BAJA. COTAS Y SUPERFICIES	EXPTE 598 - 09	ESCALA 1:100	Nº 04
PROYECTO	B DE 11 VIVIENDAS, LOCALES, GARAJE Y TRASTEROS	FECHA JULIO - 09	SUSTITUYE A	
PROMOTOR	PROMARHOGAR INFANTE S.L.	 VISADO Normal Colegio Oficial de Arquitectos de Murcia Visado Telemático Autores: JUAN SANCHEZ CARRILLO		
SITUACION	AV/ MIGUEL INDURAIN Y OTRA			
JUAN SÁNCHEZ CARRILLO		ARQUITECTO		


VISADO
Normal
Colegio Oficial de Arquitectos de Murcia
Visado Telemático
Autores: JUAN SANCHEZ CARRILLO

16/07/2009
155530/40727
MMPG

El Colegio garantiza la firma digital de los autores

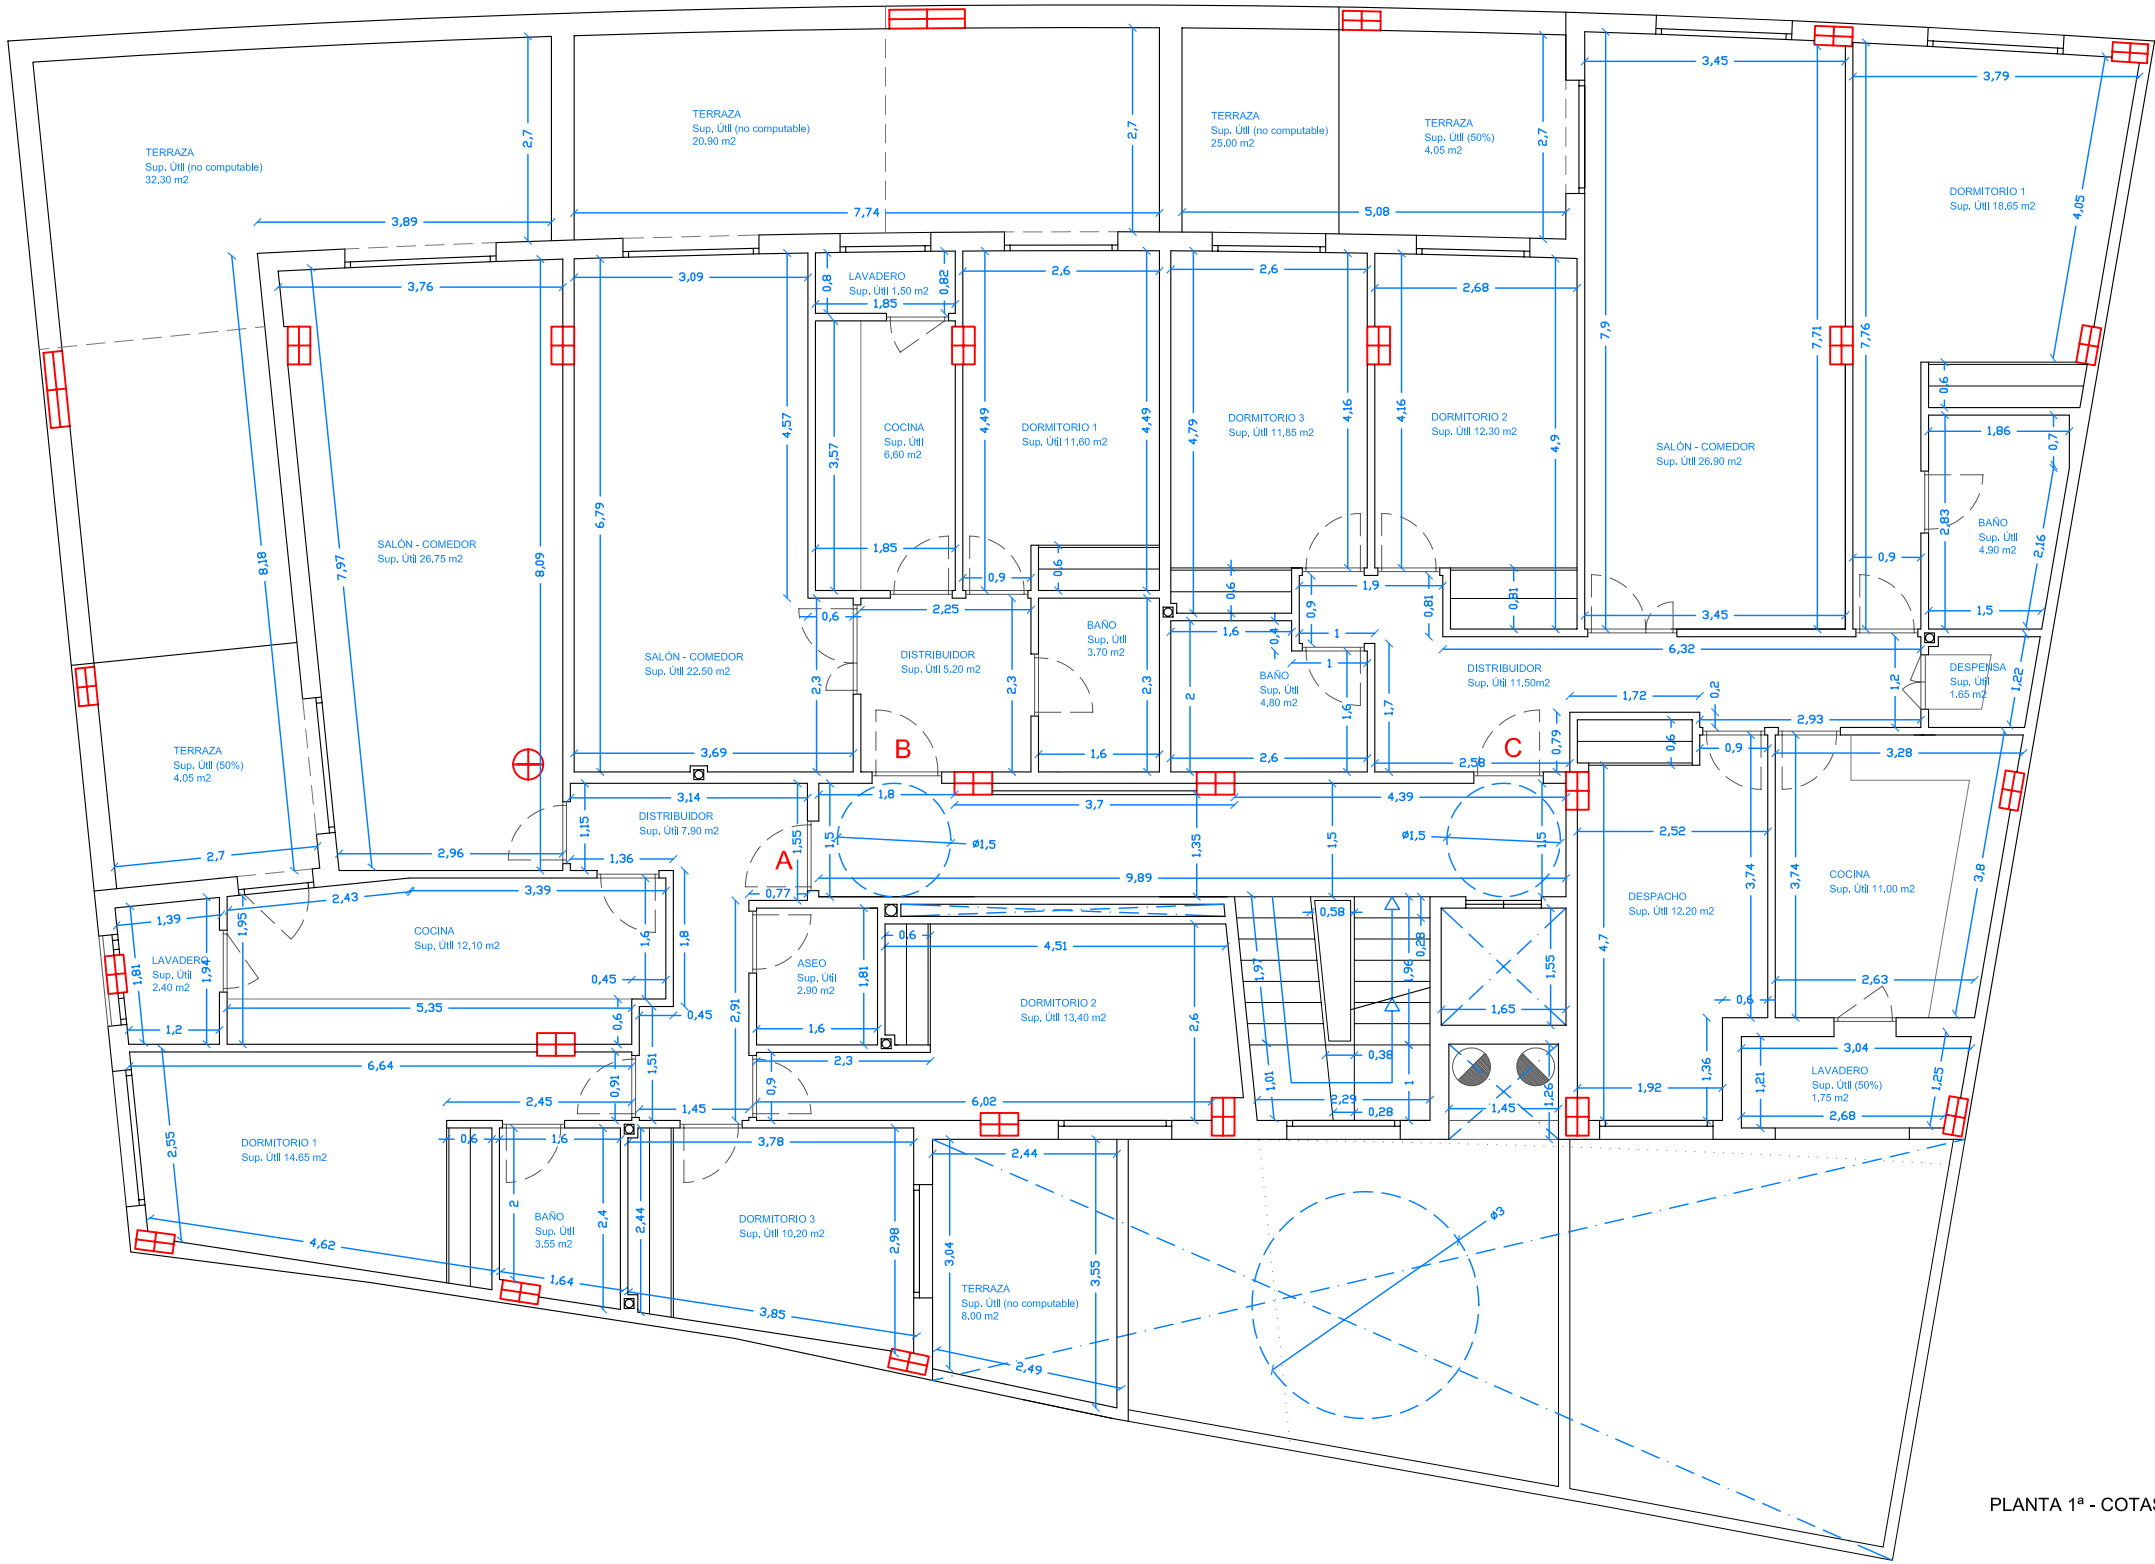

PLANTA 1ª - COTAS Y SUPERFICIES E/1:100

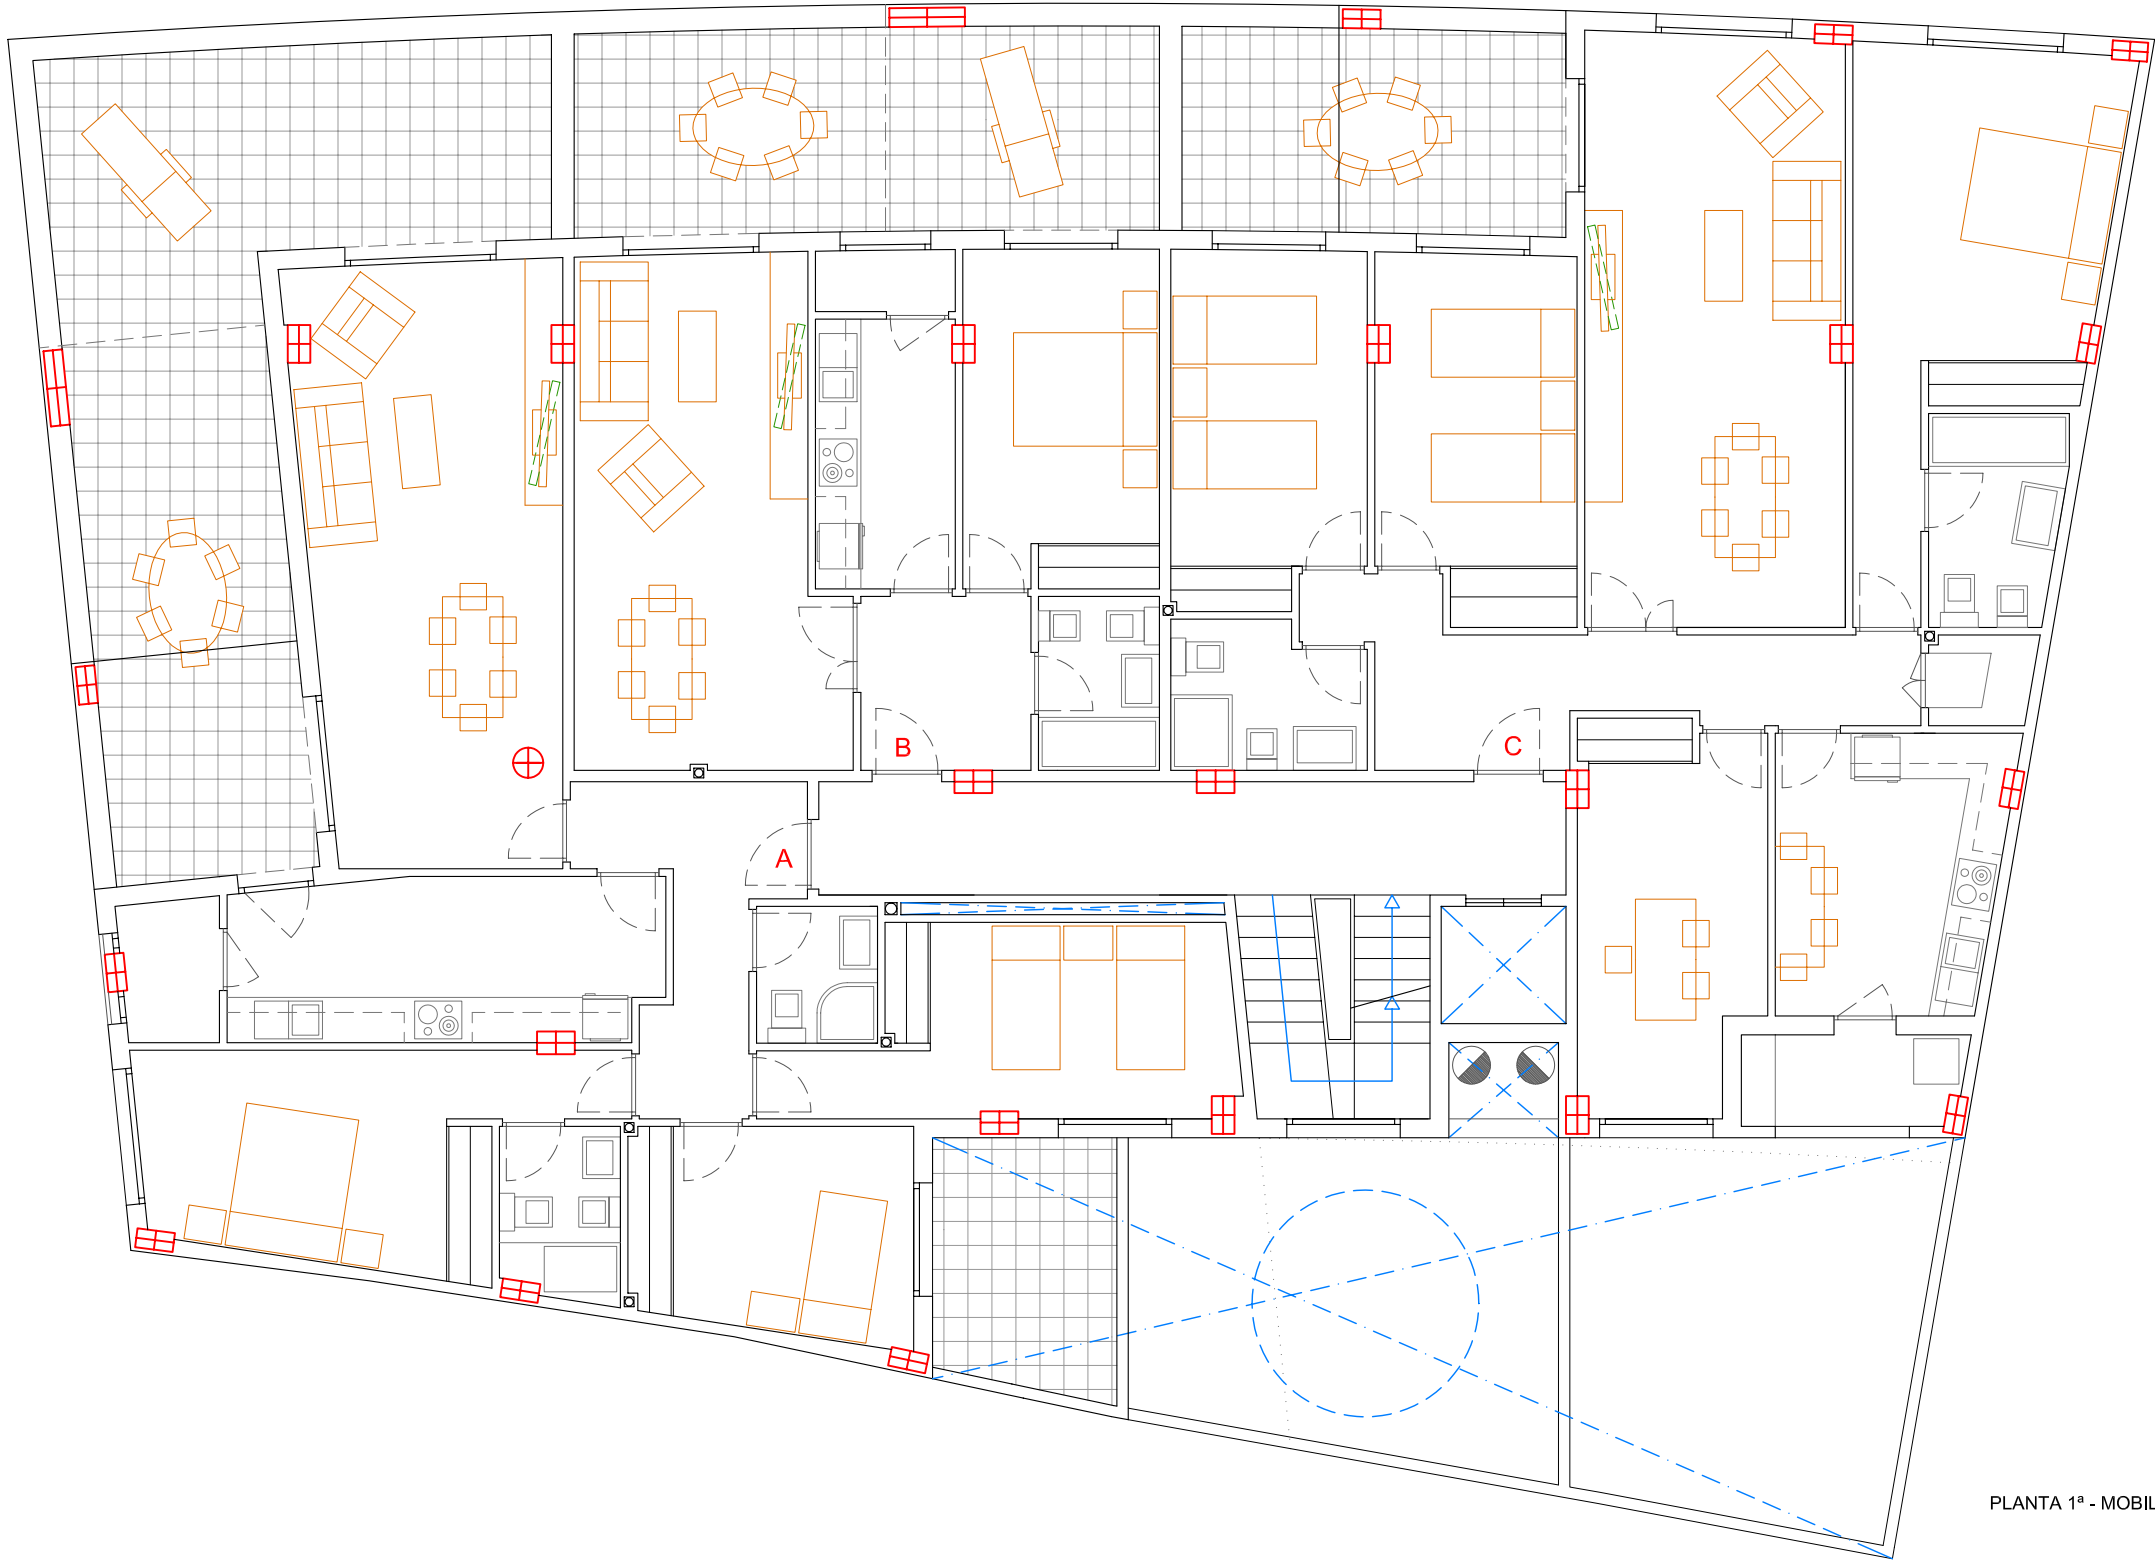

PLANTA 1ª - MOBILIARIO E/1:100


CUADRO DE SUPERFICIES DE VIVIENDA				
PLANTA	TIPO	SUP. ÚTIL	SUP. CONSTRUIDA	SUP. TERRAZAS (No computable)
PRIMERA	A	97.90 m2	131.00 m2	40.30 m2
	B	51.10 m2	68.35 m2	20.90 m2
	C	121.55 m2	162.63 m2	5.60 m2
SEGUNDA Y TERCERA	A	97.50 m2	130.42 m2	---
	B	51.10 m2	68.35 m2	---
	C	121.15 m2	162.06 m2	---
ATICO	A	97.90 m2	131.00 m2	20.45 m2
	B	51.10 m2	68.35 m2	105.55 m2
TOTAL	11 Viv.	943.30 m2	1261.88 m2	192.80m2

PLANO	PLANTA 1ª. MOBILIARIO - COTAS Y SUPERFICIES	EXPTE 598 - 09	ESCALA 1:100	Nº 05
PROYECTO	B DE 11 VIVIENDAS, LOCALES, GARAJE Y TRASTEROS	FECHA JULIO - 09	SUSTITUYE A	
PROMOTOR	PROMARHOGAR INFANTE S.L.			
SITUACION	AV/ MIGUEL INDURAIN Y OTRA			
JUAN SÁNCHEZ CARRILLO		ARQUITECTO		


VISADO
Normal
Colegio Oficial de Arquitectos de Murcia
Visado Telemático
Autores: JUAN SANCHEZ CARRILLO

16/07/2009
155530/40727
MMPG

El Colegio garantiza la firma digital de los autores

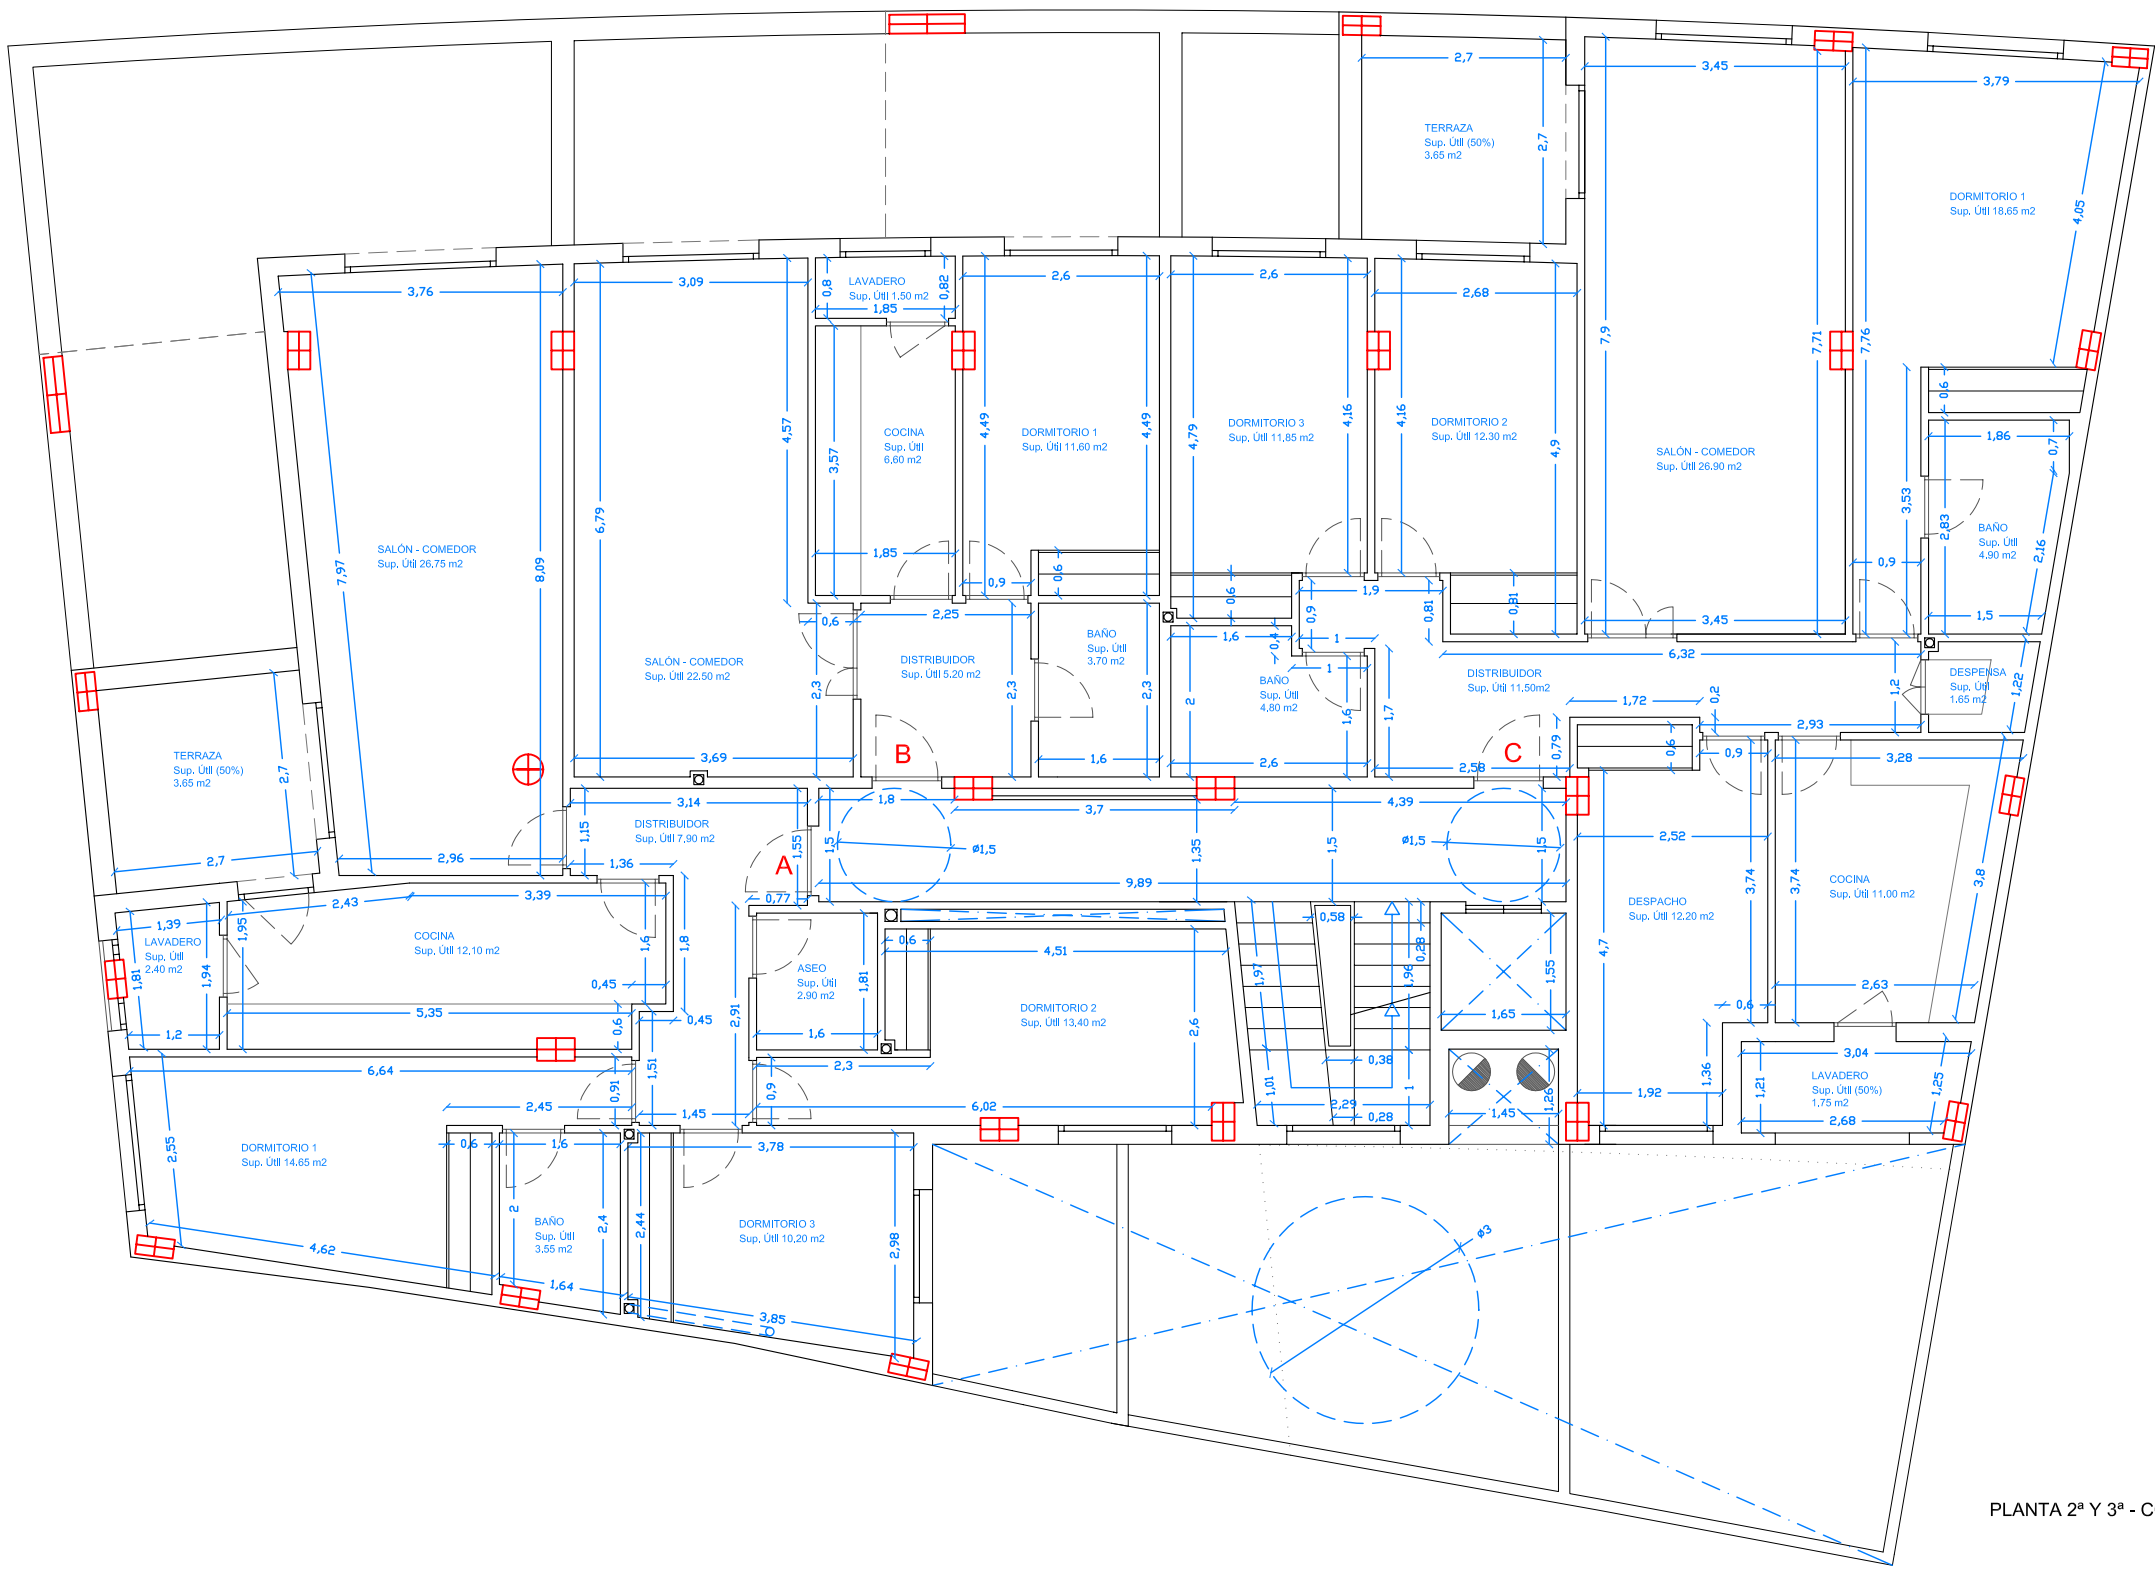

PLANTA 2ª Y 3ª - COTAS Y SUPERFICIES E/1:100

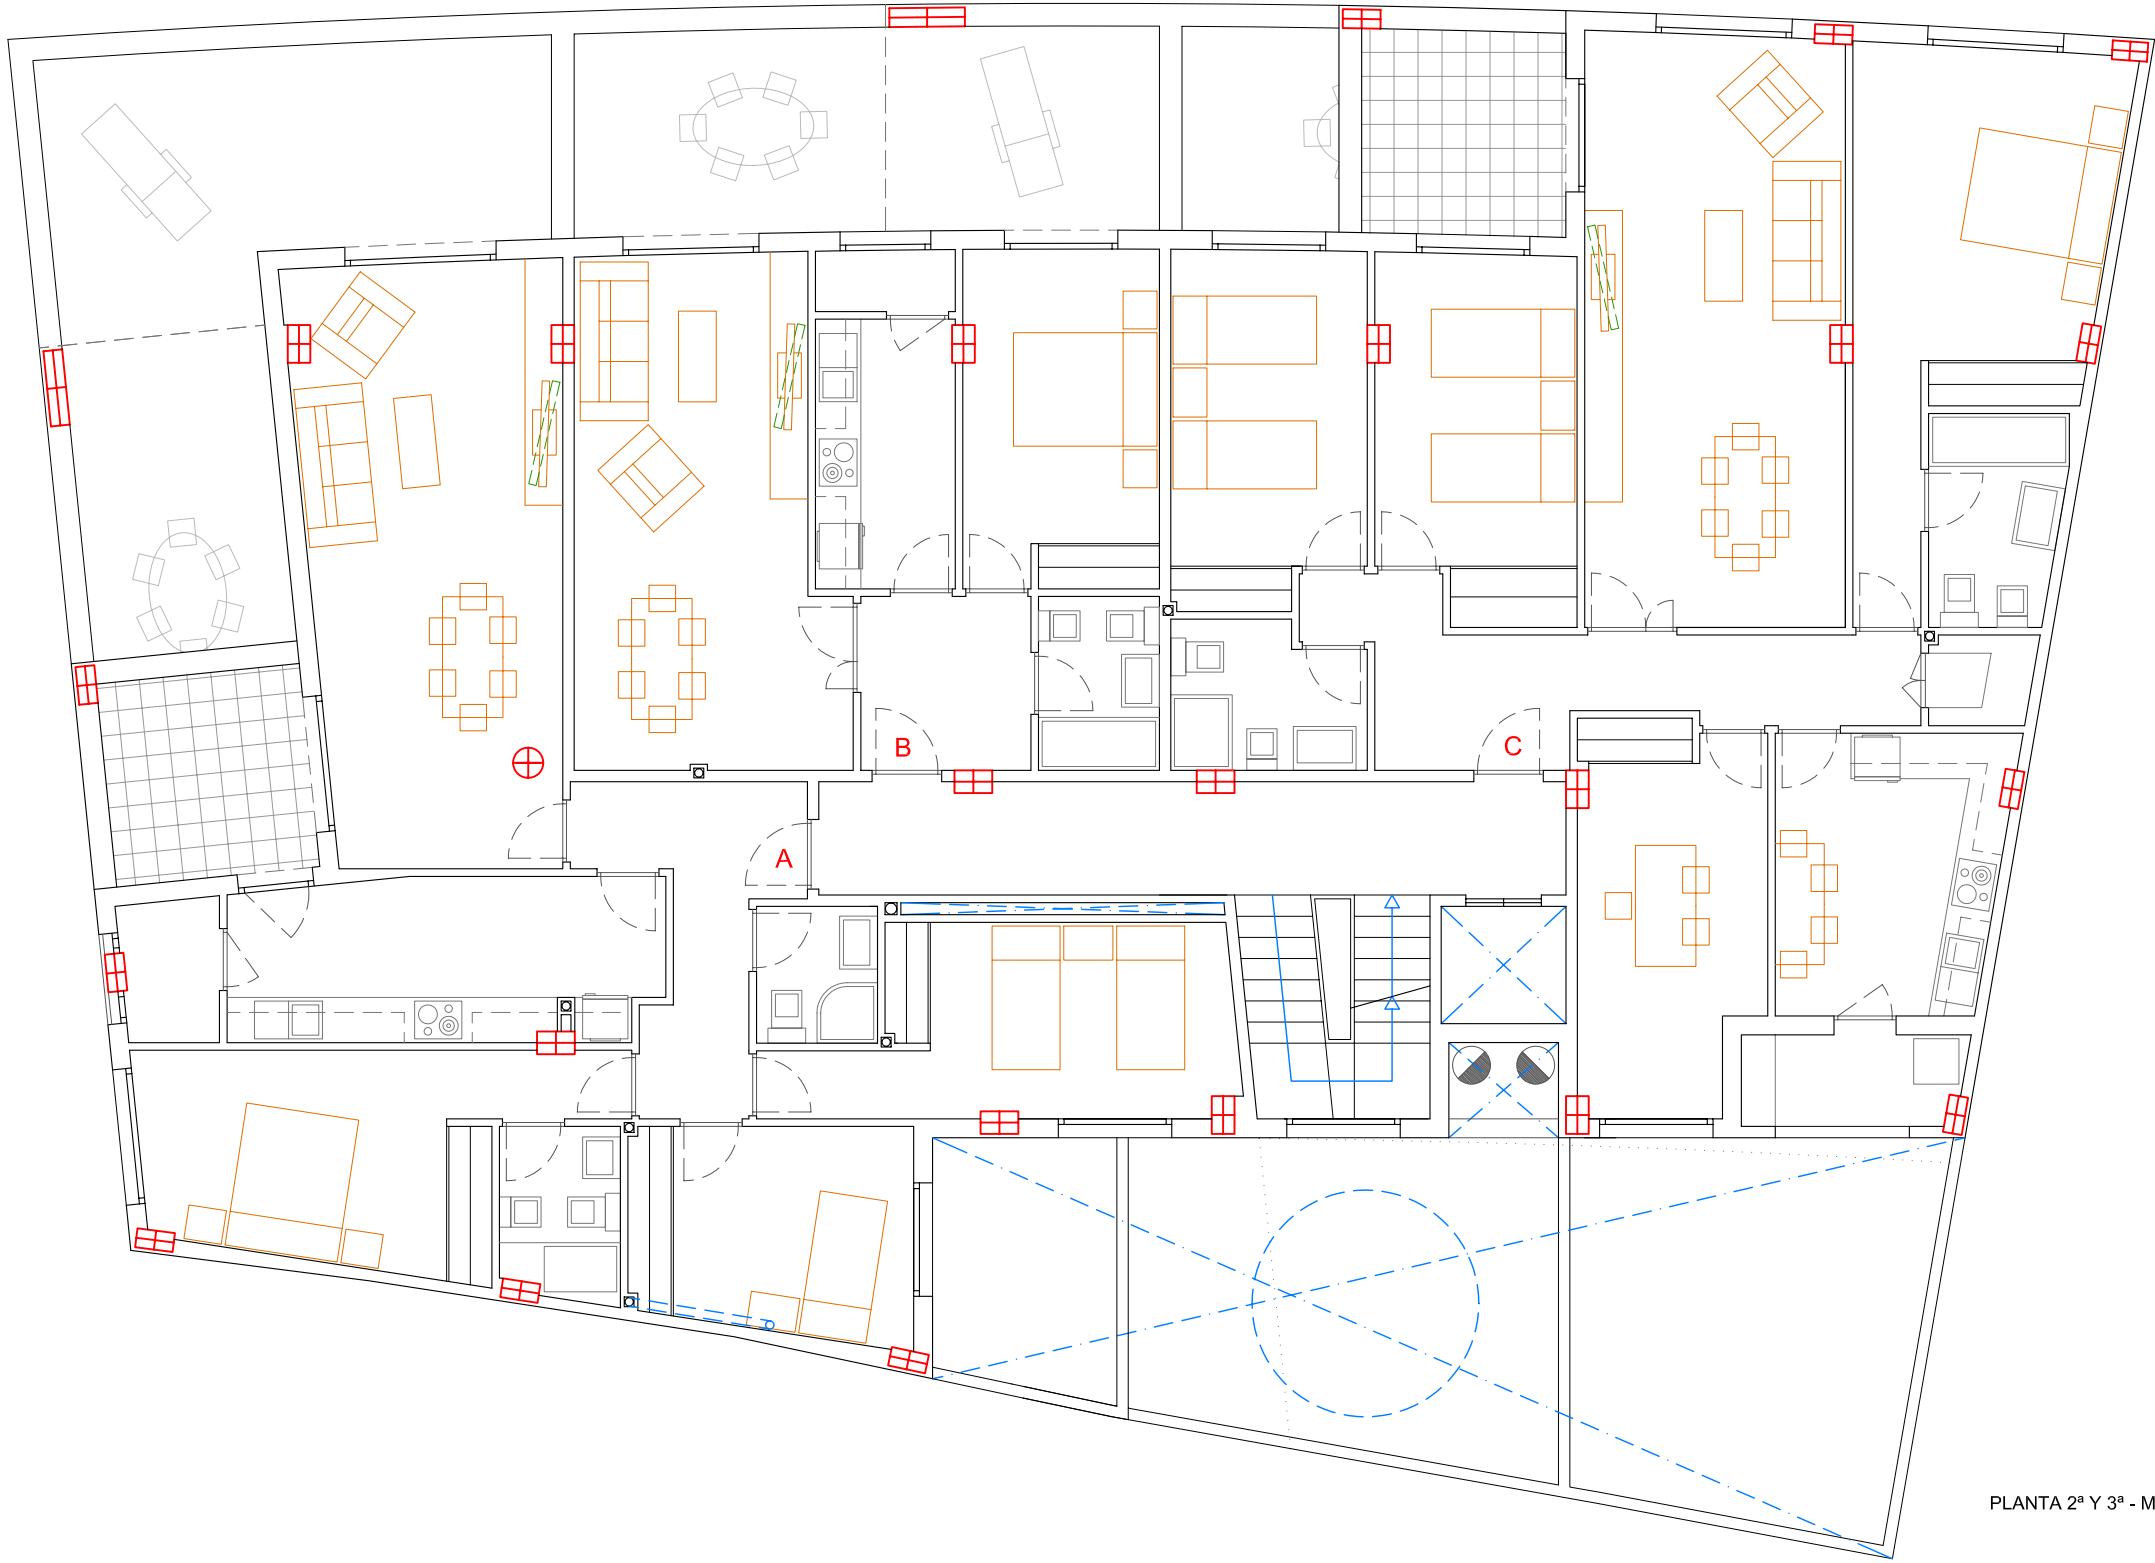

PLANTA 2ª Y 3ª - MOBILIARIO E/1:100


CUADRO DE SUPERFICIES DE VIVIENDA				
PLANTA	TIPO	SUP. ÚTIL	SUP. CONSTRUIDA	SUP. TERRAZAS (No computable)
PRIMERA	A	97.90 m2	131.00 m2	40.30 m2
	B	51.10 m2	68.35 m2	20.90 m2
	C	121.55 m2	162.63 m2	5.60 m2
SEGUNDA Y TERCERA	A	97.50 m2	130.42 m2	---
	B	51.10 m2	68.35 m2	---
	C	121.15 m2	162.06 m2	---
ATICO	A	97.90 m2	131.00 m2	20.45 m2
	B	51.10 m2	68.35 m2	105.55 m2
TOTAL	11 Viv.	943.30 m2	1261.88 m2	192.80 m2

PLANO	PLANTAS 2ª Y 3ª. MOBILIARIO - COTAS Y SUPERFICIES	EXPTE 598 - 09	ESCALA 1:100	Nº 06
PROYECTO	B DE 11 VIVIENDAS, LOCALES, GARAJE Y TRASTEROS	FECHA JULIO - 09	SUSTITUYE A	
PROMOTOR	PROMARHOGAR INFANTE S.L.	 VISADO Normal Colegio Oficial de Arquitectos de Murcia Visado Telemático Autores: JUAN SANCHEZ CARRILLO		
SITUACION	AV/ MIGUEL INDURAIN Y OTRA			
JUAN SÁNCHEZ CARRILLO		ARQUITECTO		


VISADO
Normal
Colegio Oficial de Arquitectos de Murcia
Visado Telemático
Autores: JUAN SANCHEZ CARRILLO

16/07/2009
155530/40727
MMPG

El Colegio garantiza la firma digital de los autores

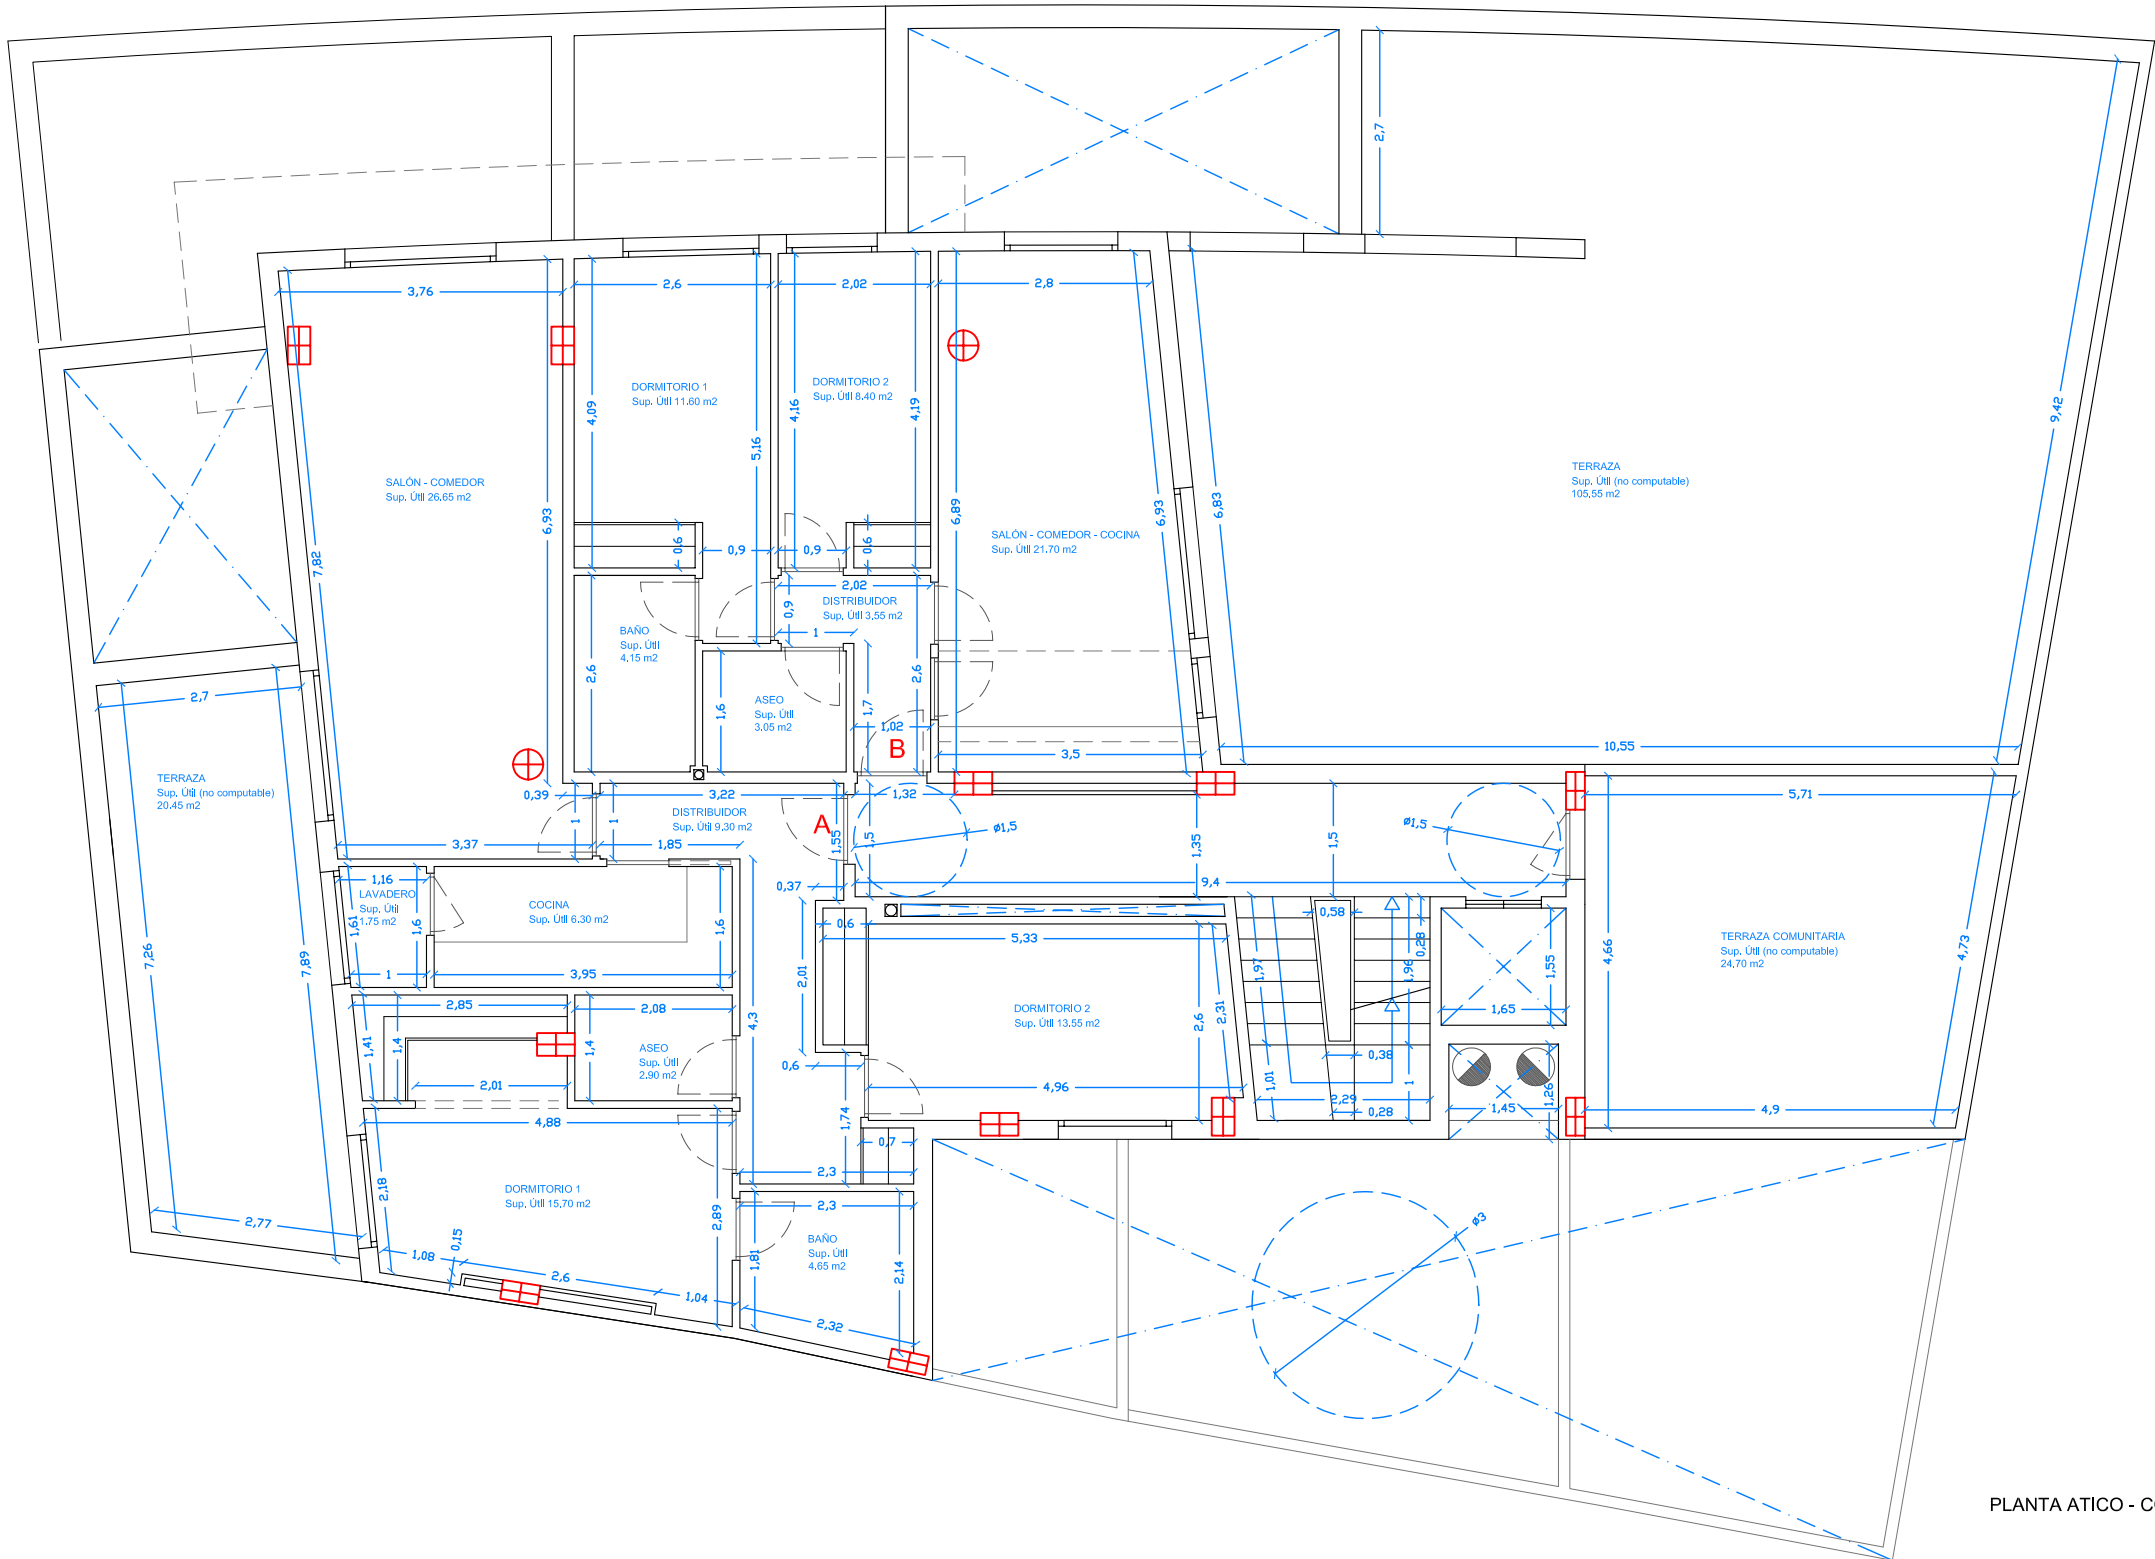

PLANTA ATICO - COTAS Y SUPERFICIES E/1:100

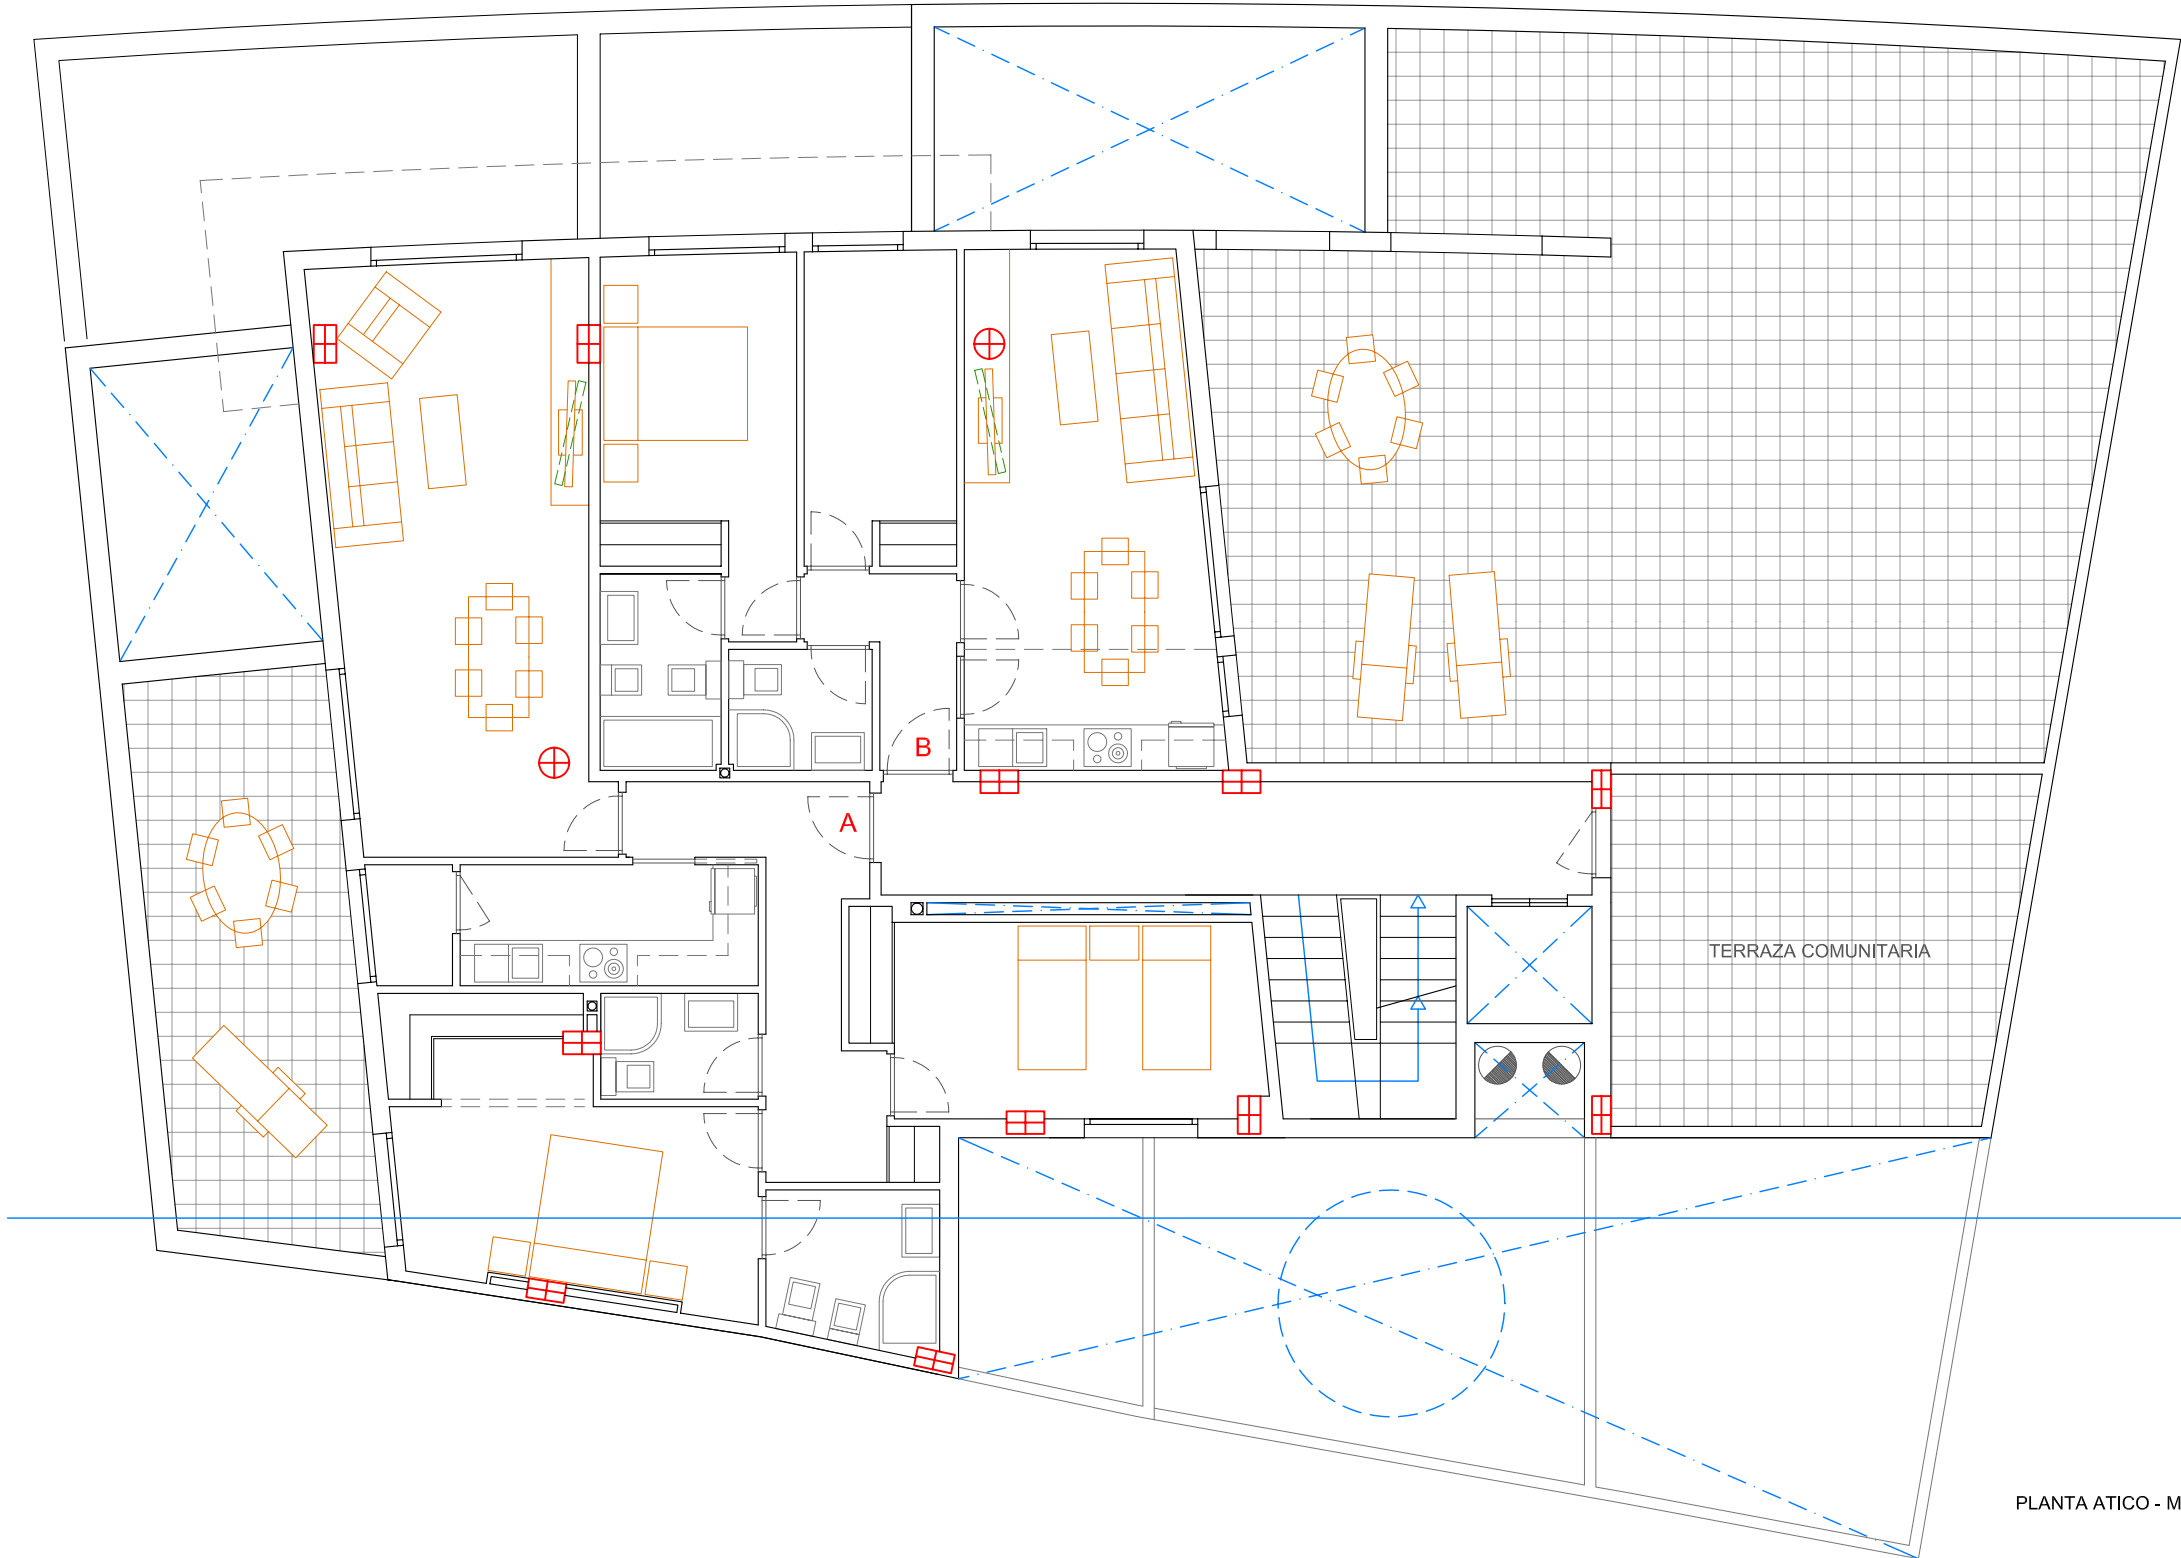

PLANTA ATICO - MOBILIARIO E/1:100


CUADRO DE SUPERFICIES DE VIVIENDA				
PLANTA	TIPO	SUP. ÚTIL	SUP. CONSTRUIDA	SUP. TERRAZAS (No computable)
PRIMERA	A	97.90 m2	131.00 m2	40.30 m2
	B	51.10 m2	68.35 m2	20.90 m2
	C	121.55 m2	162.63 m2	5.60 m2
SEGUNDA Y TERCERA	A	97.50 m2	130.42 m2	---
	B	51.10 m2	68.35 m2	---
	C	121.15 m2	162.06 m2	---
ATICO	A	97.90 m2	131.00 m2	20.45 m2
	B	51.10 m2	68.35 m2	105.55 m2
TOTAL	11 Viv.	943.30 m2	1261.88 m2	192.80 m2

PLANO	PLANTA ATICO. MOBILIARIO - COTAS Y SUPERFICIES	EXYTE 598 - 09	ESCALA 1:100	Nº 07
PROYECTO	B DE 11 VIVIENDAS, LOCALES, GARAJE Y TRASTEROS	FECHA JULIO - 09	SUSTITUYE A	
PROMOTOR	PROMARHOGAR INFANTE S.L.	 VISADO Normal Colegio Oficial de Arquitectos de Murcia Visado Telemático Autores: JUAN SANCHEZ CARRILLO		
SITUACION	AV/ MIGUEL INDURAIN Y OTRA			
JUAN SÁNCHEZ CARRILLO		ARQUITECTO		

VISADO
Normal
Colegio Oficial de Arquitectos de Murcia
Visado Telemático
Autores: JUAN SANCHEZ CARRILLO


16/07/2009
155530/40727
MMPG

El Colegio garantiza la firma digital de los autores

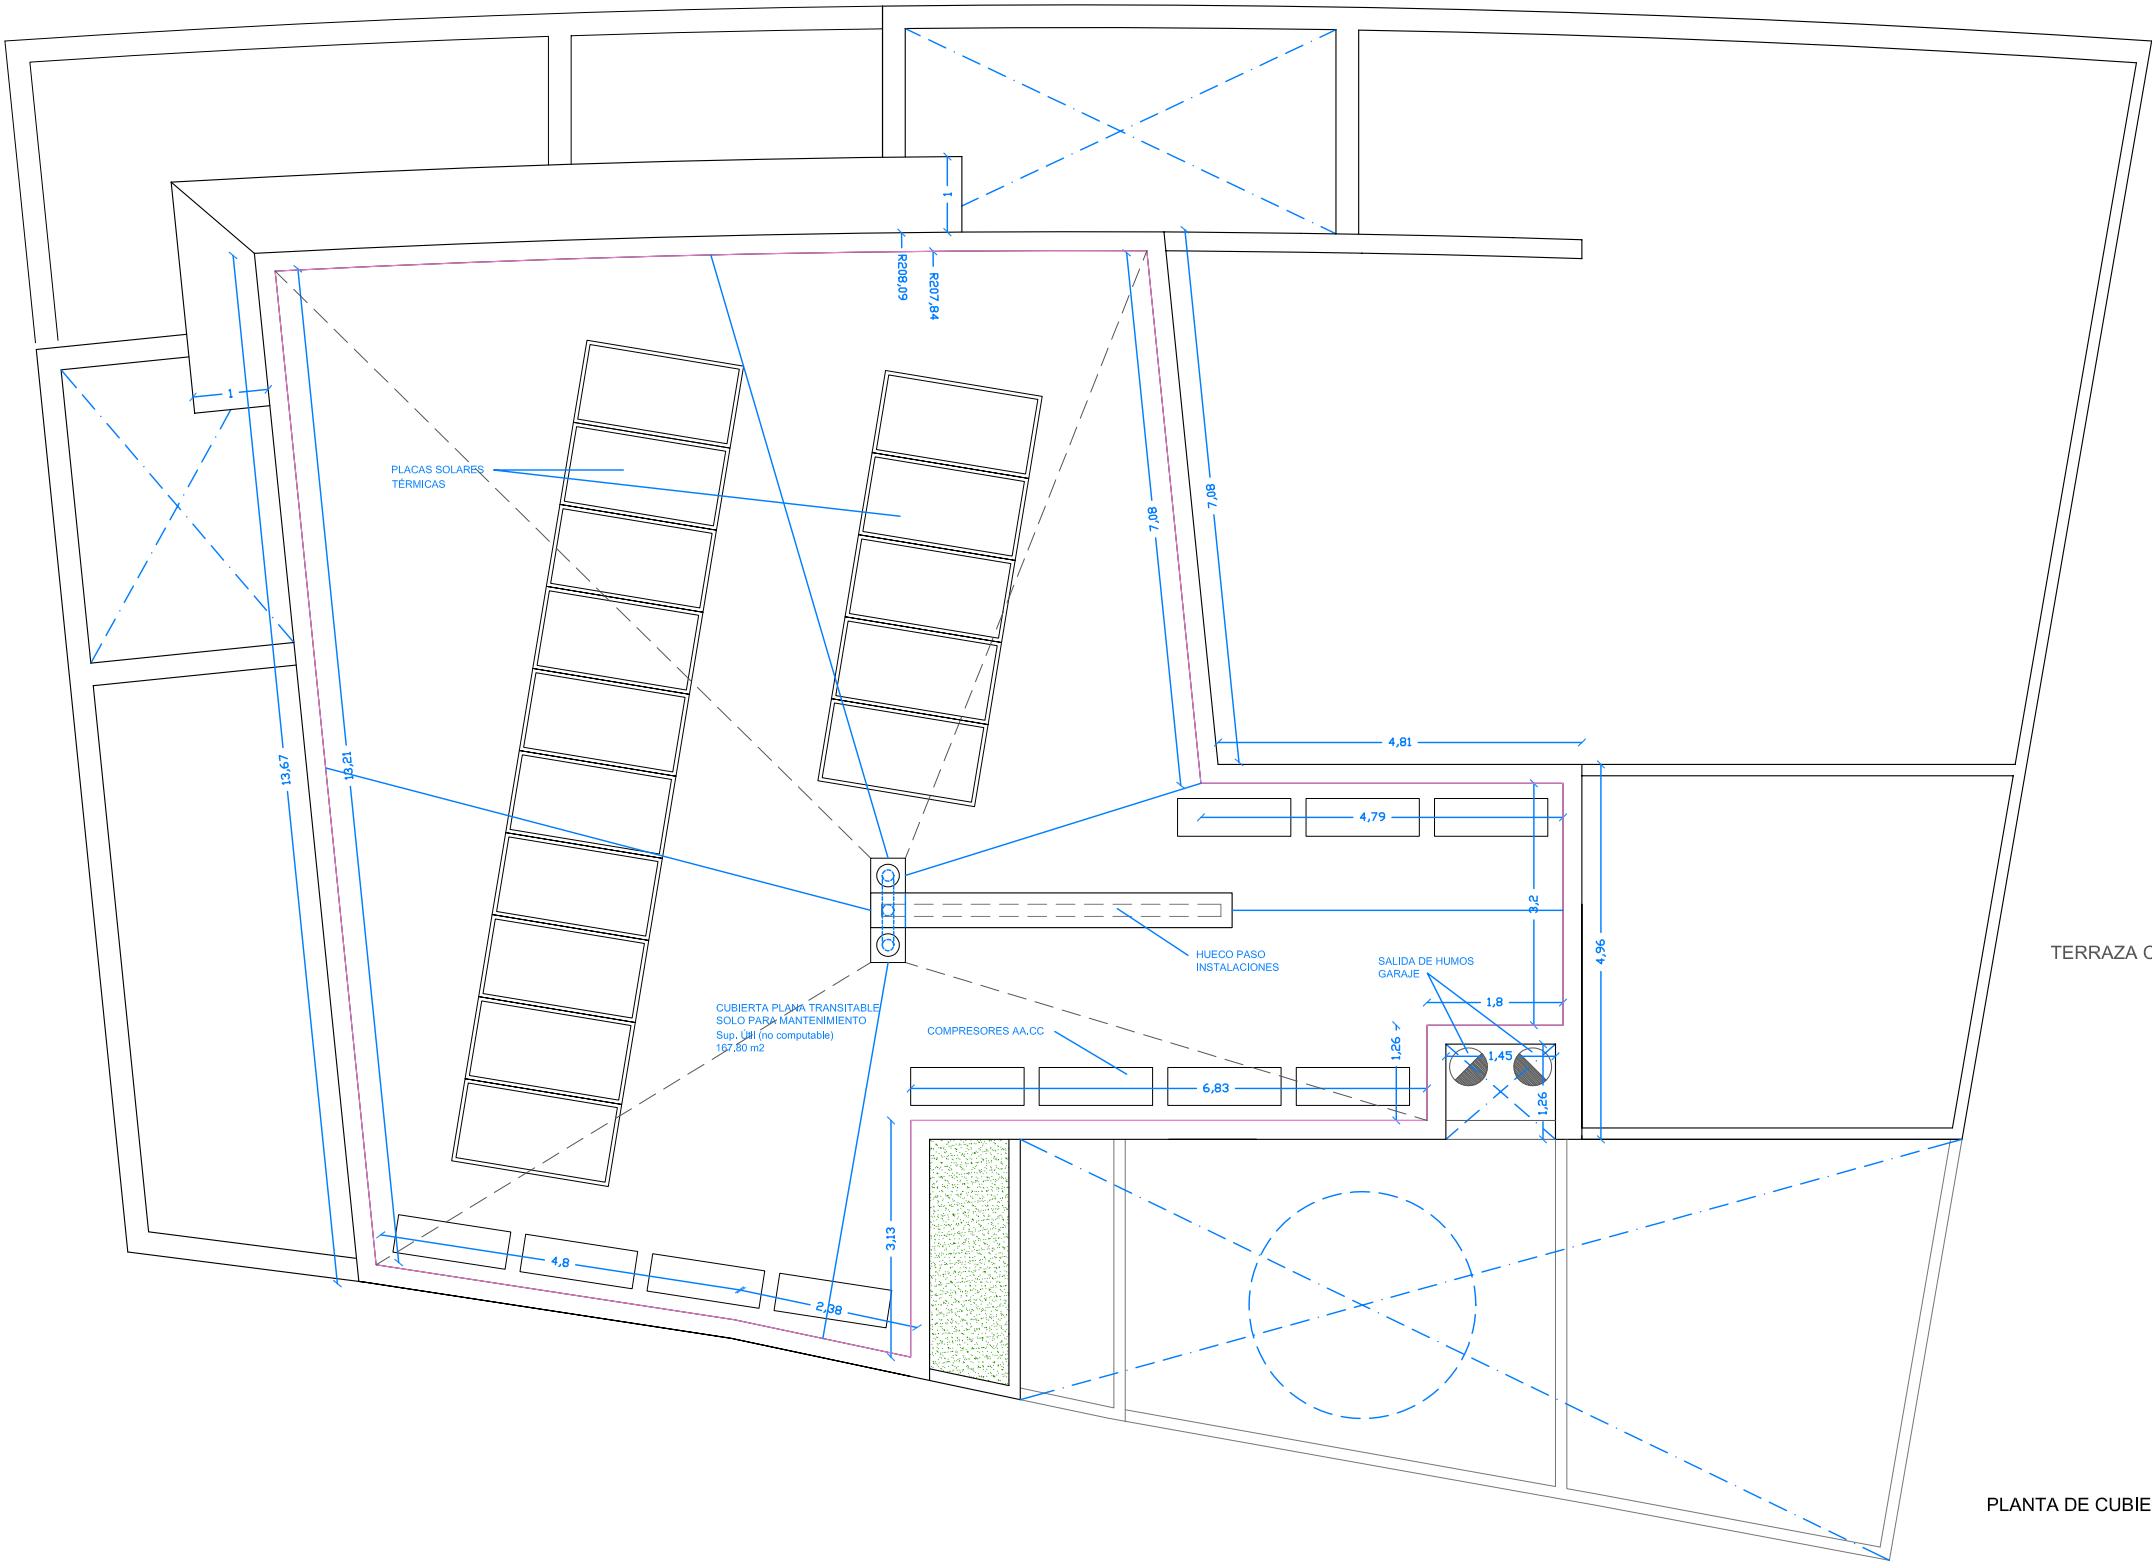

TERRAZA COMUNITARIA

PLANTA DE CUBIERTA E/1:100

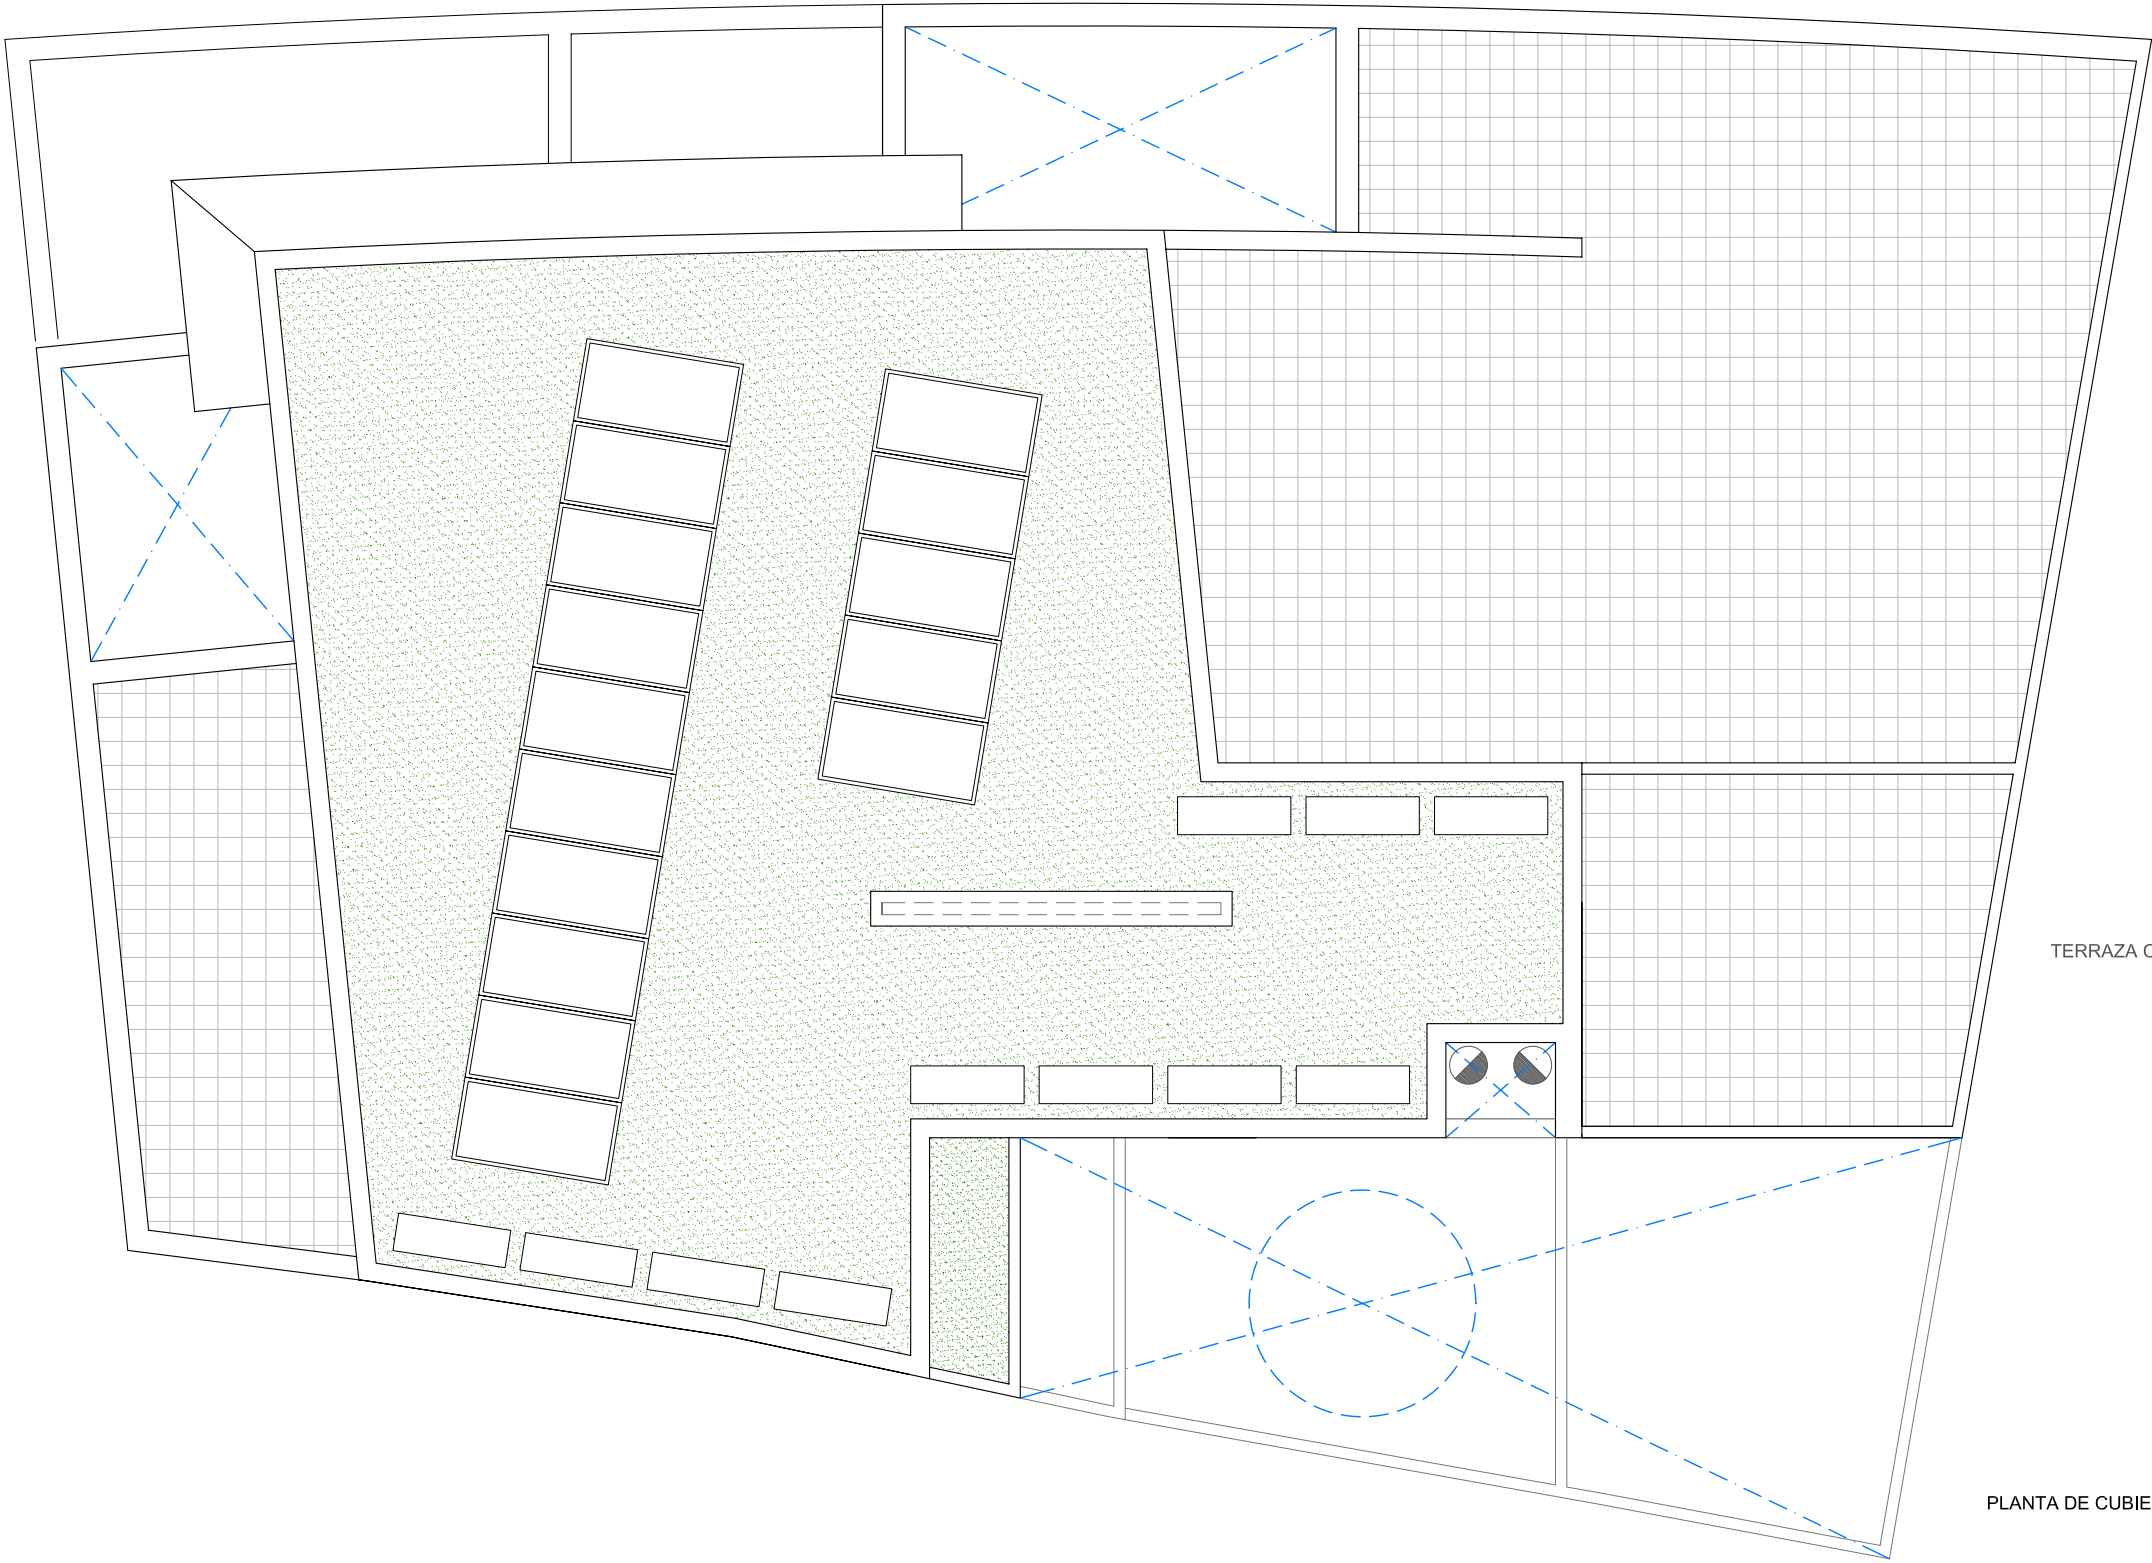

TERRAZA COMUNITARIA


PLANTA DE CUBIERTA E/1:100

PLANO	PLANTA CUBIERTA. COTAS Y SUPERFICIES	EXPTE 598 - 09	ESCALA 1:100	Nº 08
PROYECTO	B DE 11 VIVIENDAS, LOCALES, GARAJE Y TRASTEROS	FECHA JULIO - 09	SUSTITUYE A	
PROMOTOR	PROMARHOGAR INFANTE S.L.			
SITUACION	AV/ MIGUEL INDURAIN Y OTRA			
JUAN SÁNCHEZ CARRILLO ARQUITECTO				





VISADO
Normal
Colegio Oficial de Arquitectos de Murcia
Visado Telemático
Autores: JUAN SANCHEZ CARRILLO


16/07/2009
155530/40727
MMPG

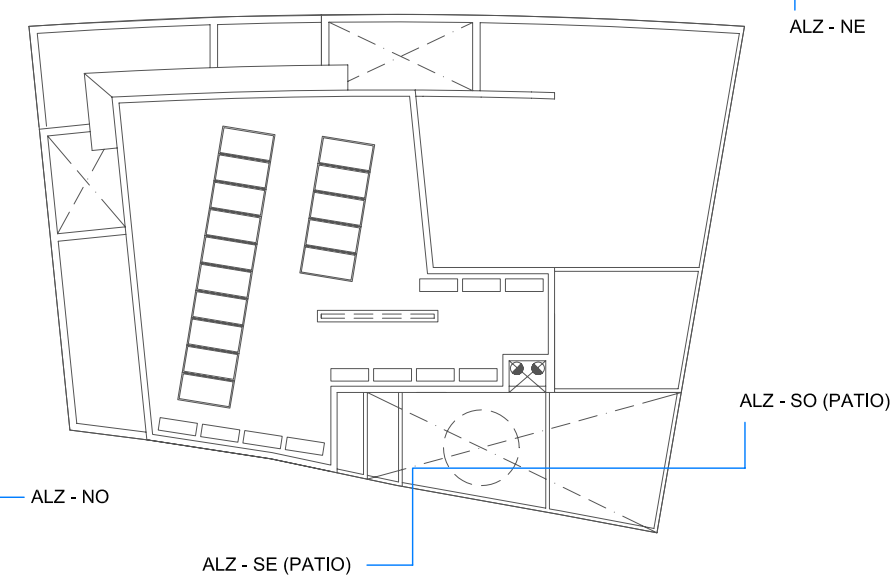


VISADO
 Normal
 16/07/2009
 155530140727
 Colegio Oficial de Arquitectos de Murcia
 Autores: JUAN SANCHEZ CARRILLO

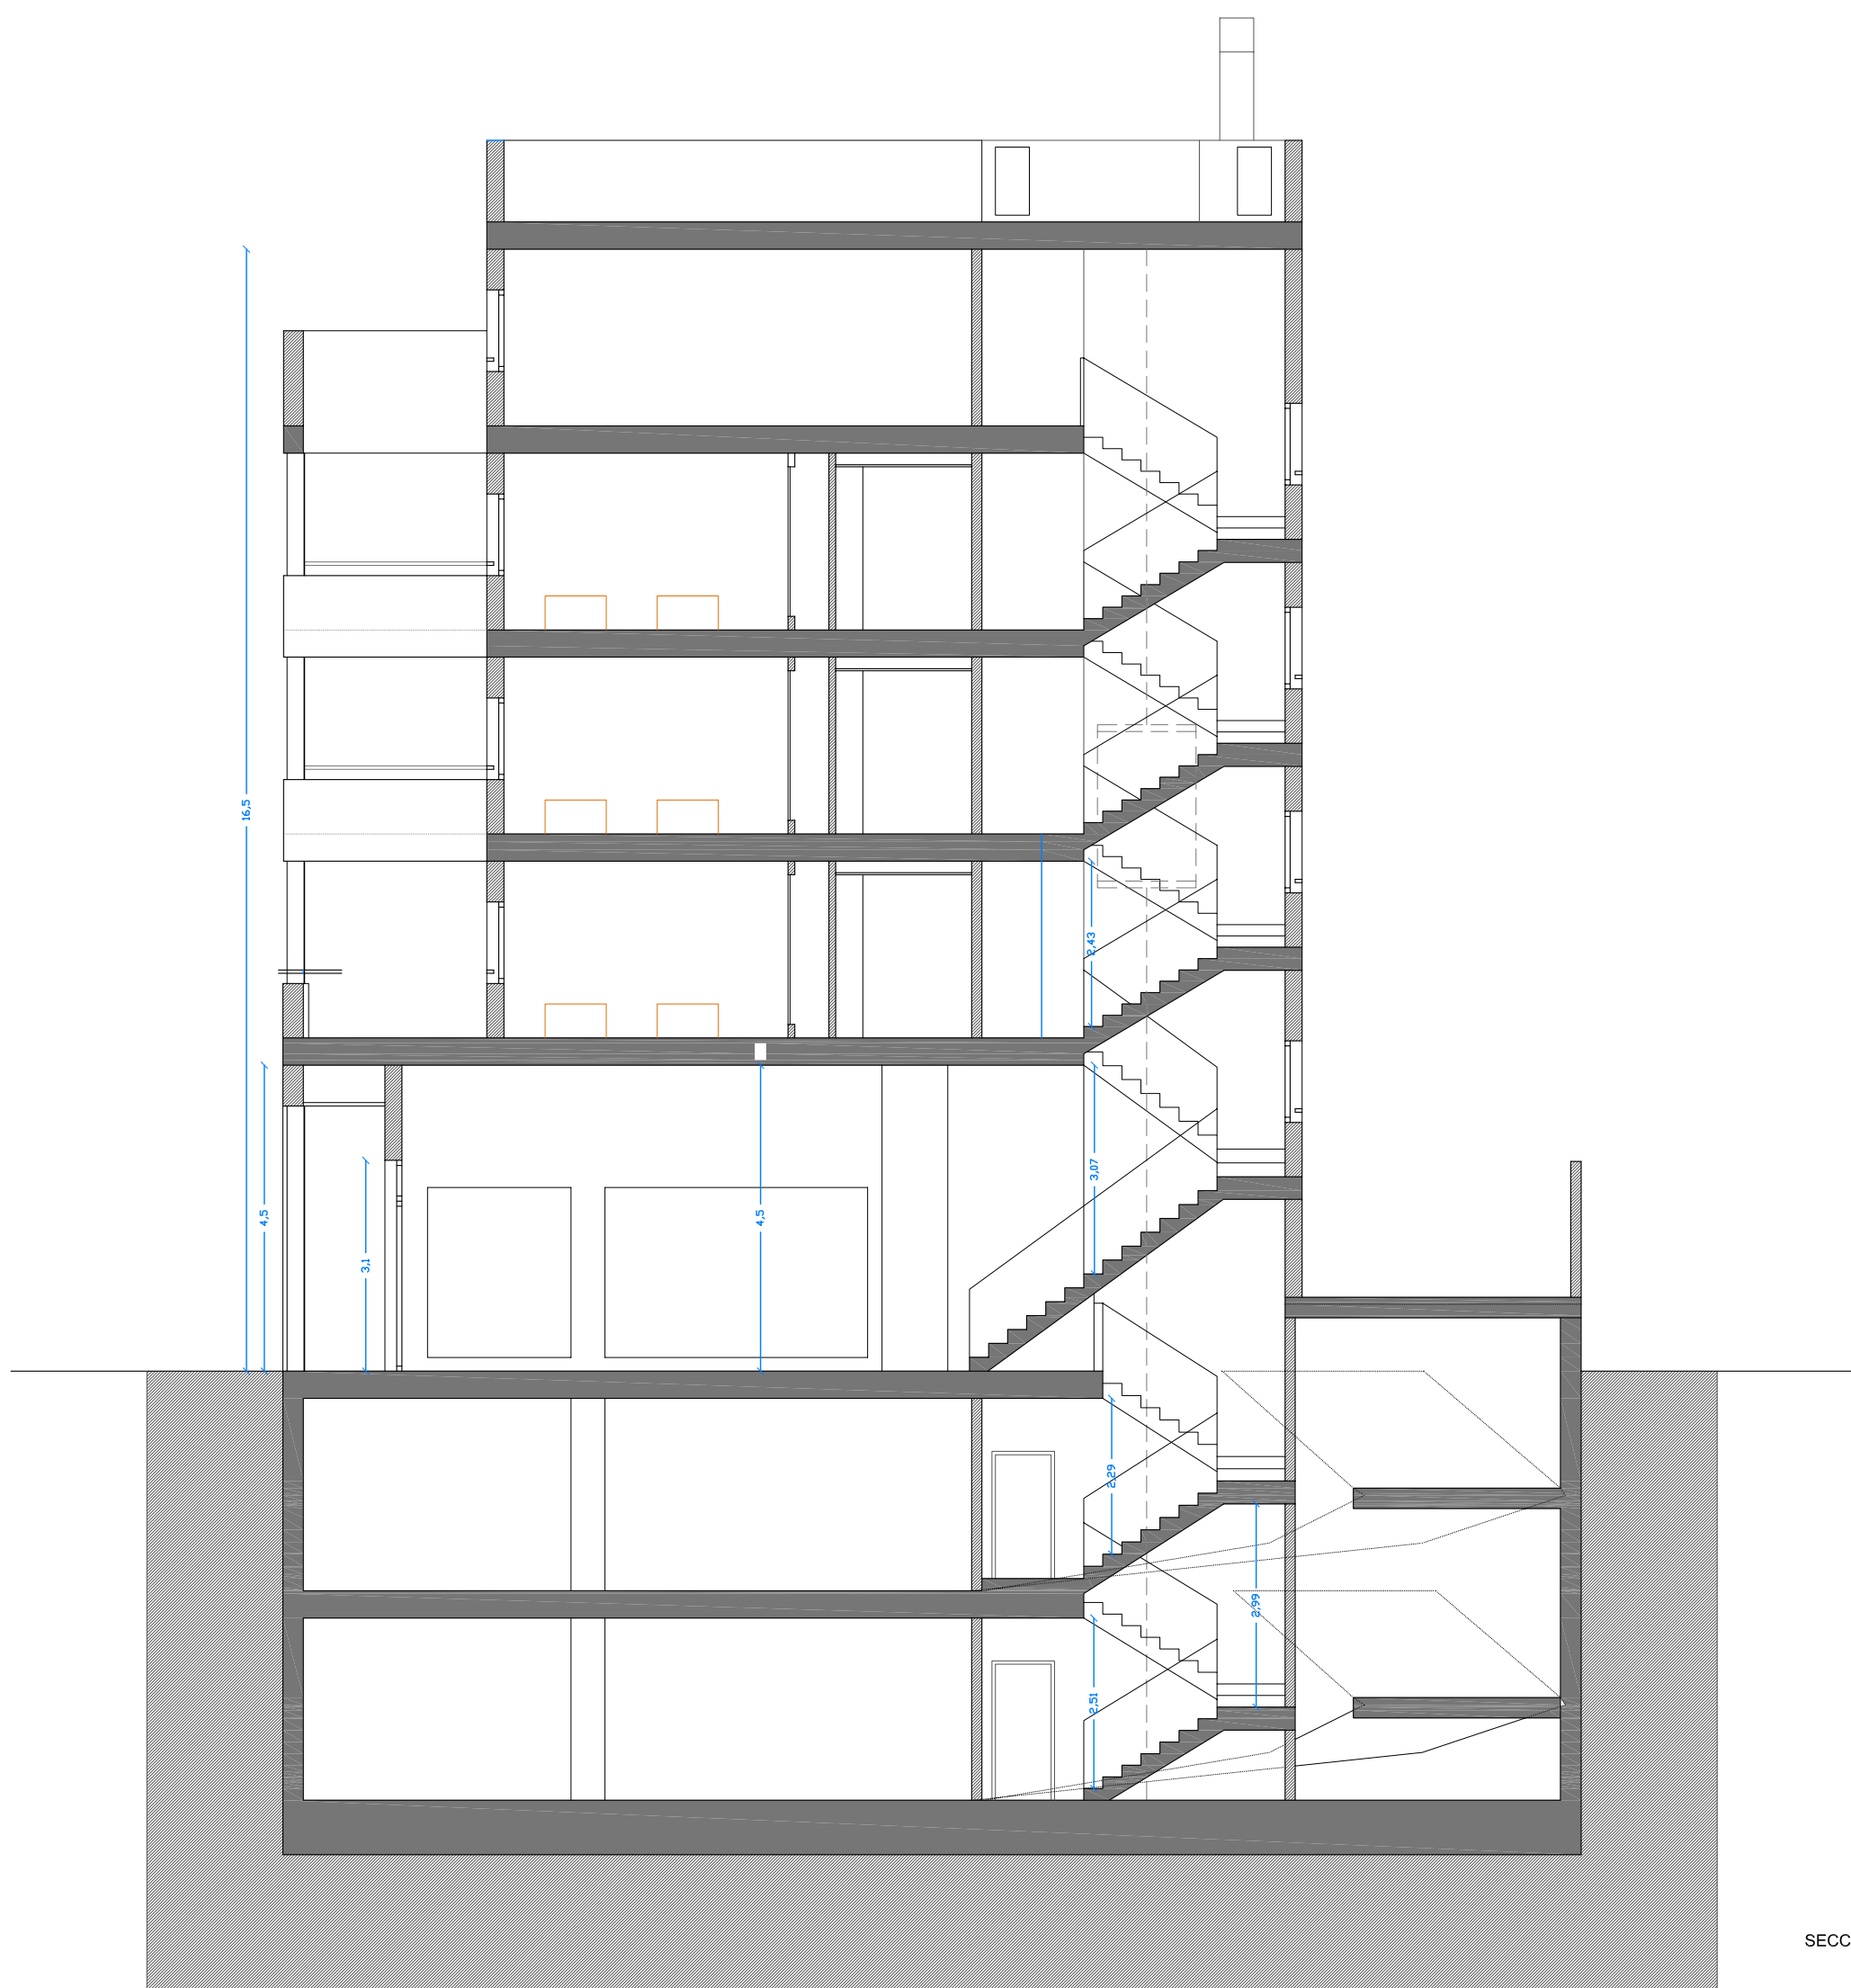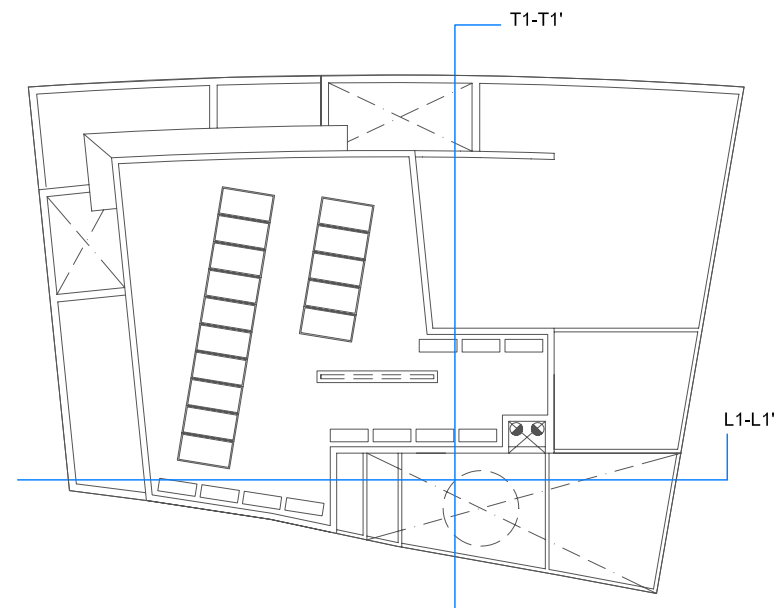

SECCION TRANSVERSAL T1-T1' E/1:100

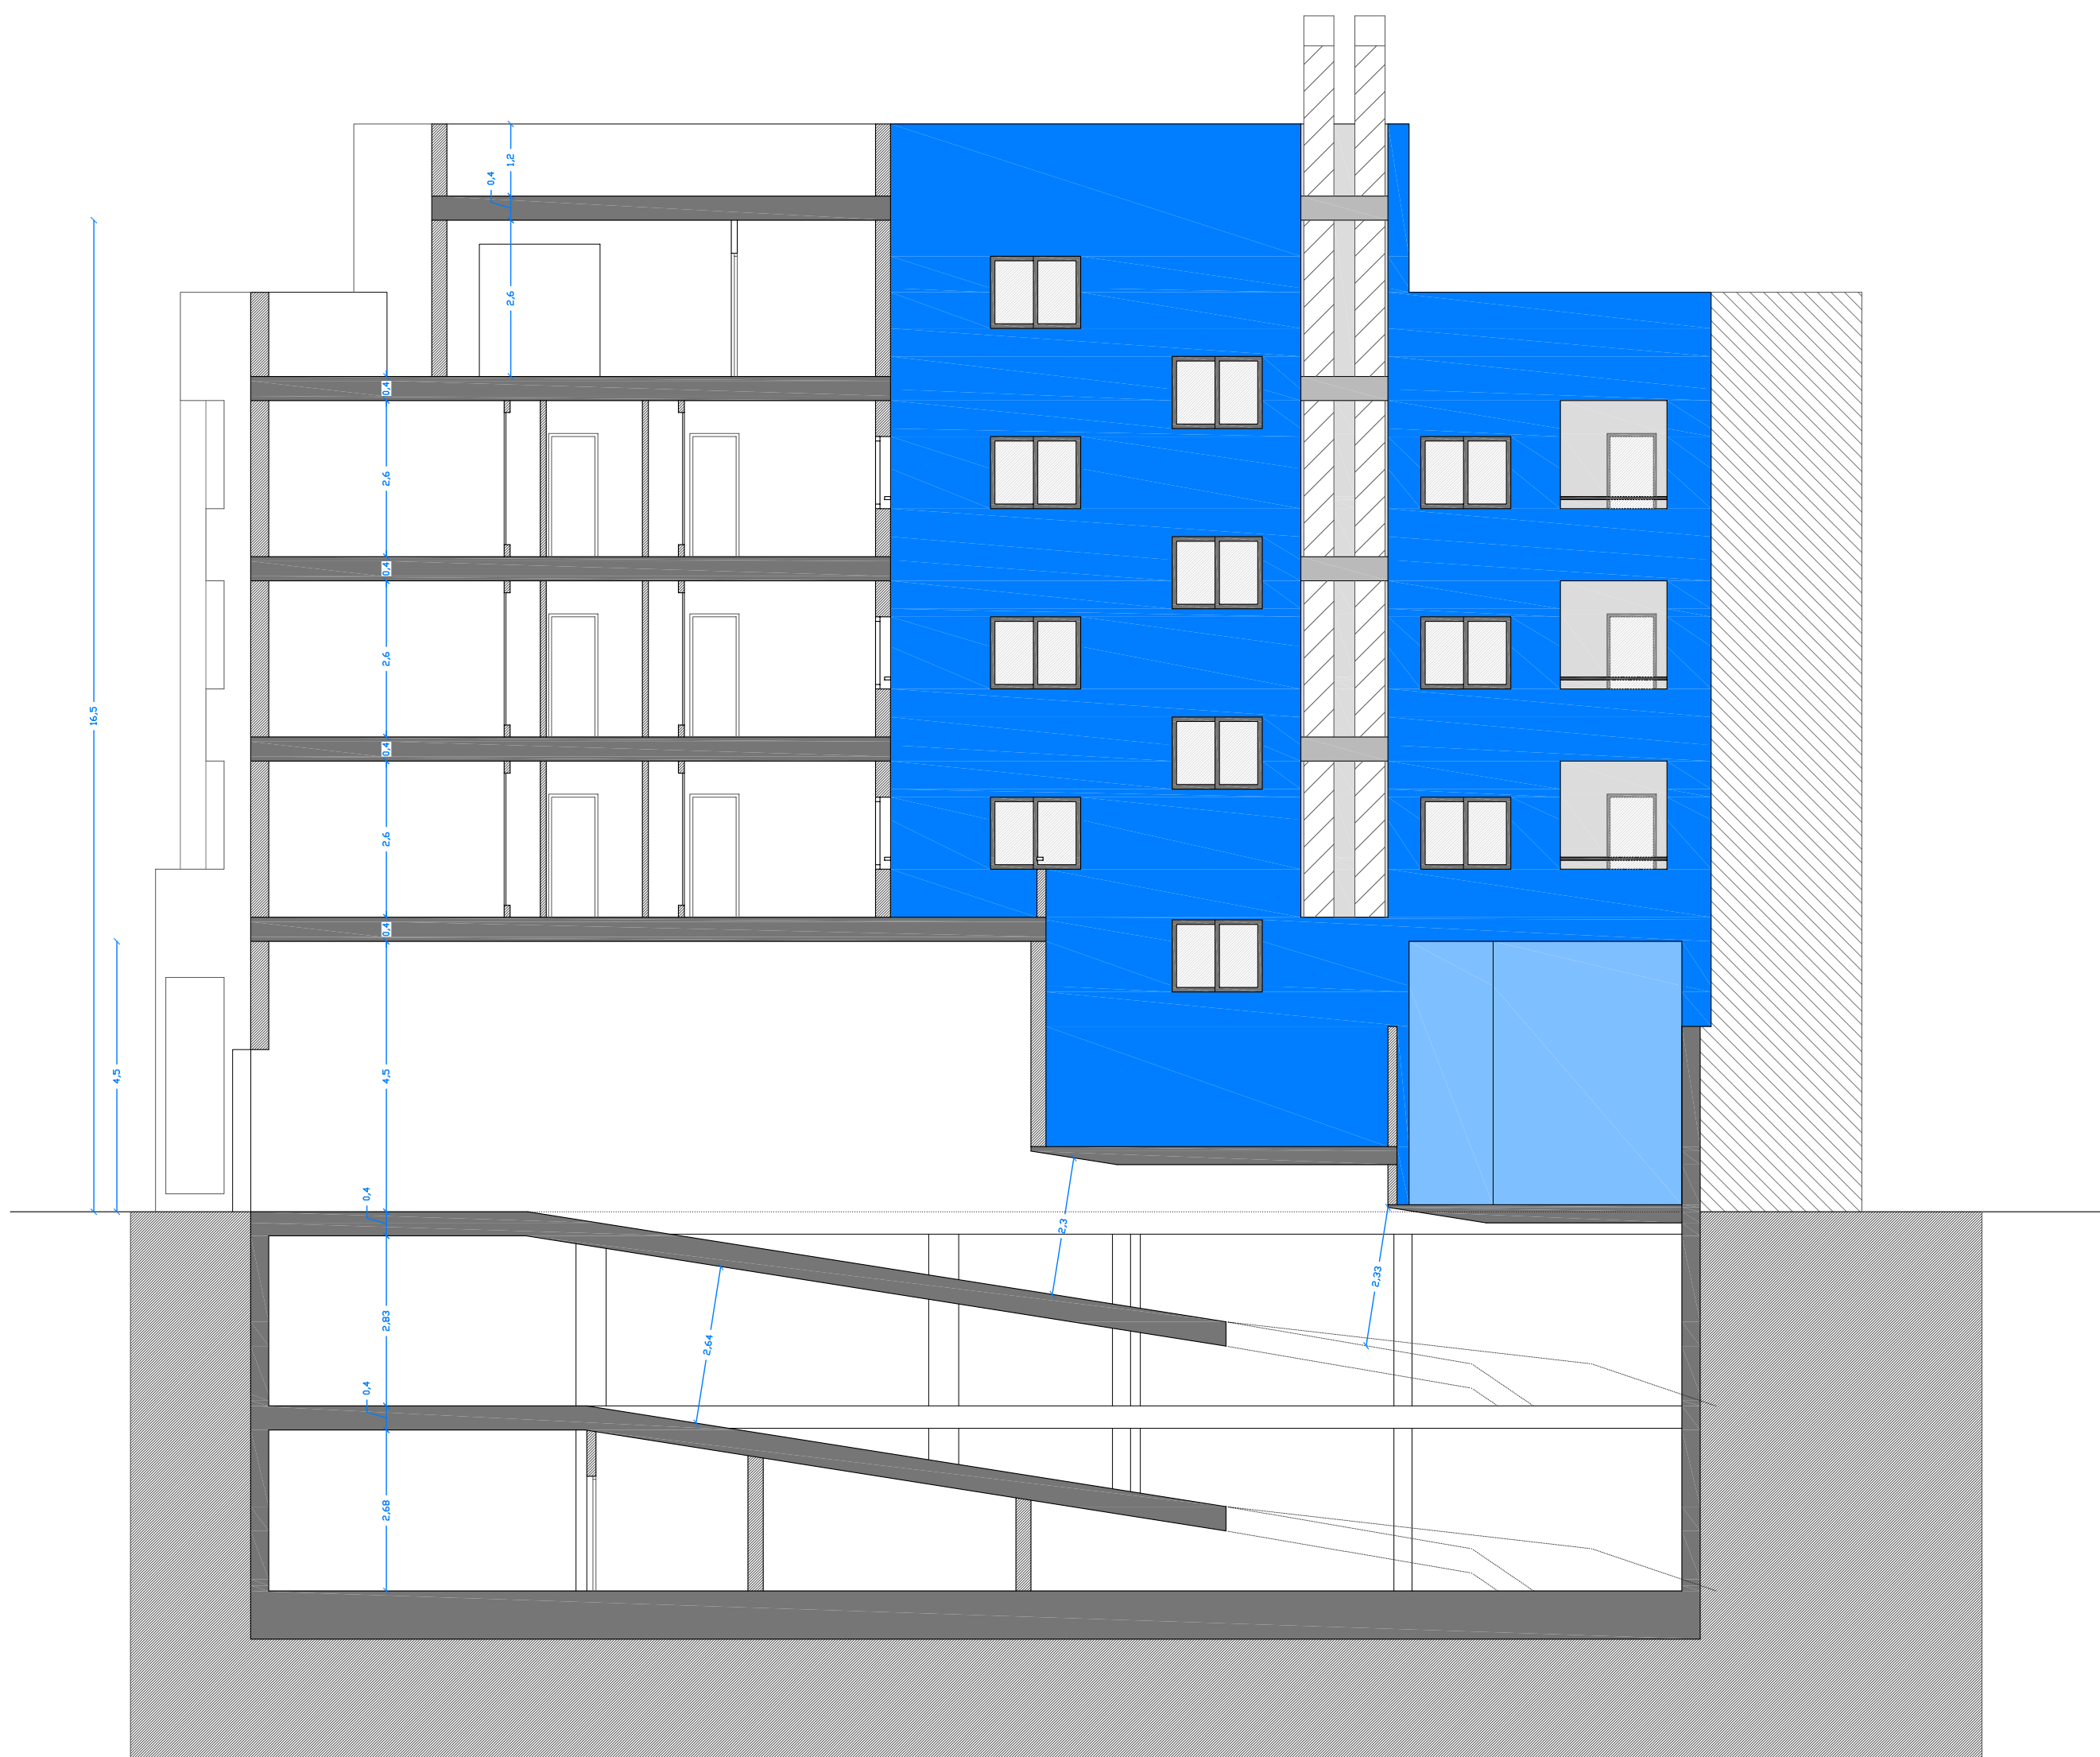

SECCION LONGITUDINAL L1-L1' E/1:100

PLANO	SECCIONES	EXPRE	598 - 09	ESCALA	1:100	Nº	10
PROYECTO	B DE 11 VIVIENDAS, LOCALES, GARAJE Y TRASTEROS		FECHA	JULIO - 09		SUSCRITURA	
PROMOTOR	PROMARHOGAR INFANTE S.L.						
SITUACION	AV/ MIGUEL INDURAIN Y OTRA						
JUAN SÁNCHEZ CARRILLO		ARQUITECTO		 VISADO Normal Colegio Oficial de Arquitectos de M Visado Tecnológico Autres: JUAN SANCHEZ CARRILLO			

VISADO
Normal
Colegio Oficial de Arquitectos de Murcia
Visado Telemático
Autores: JUAN SANCHEZ CARRILLO

16/07/2009
155530/40727
MMPG